



FINSHING
Schedule

1-FLORING	
CODE	
1	CERAMIC TILES 40*40*0.4CM
2	CERAMIC TILES 20*20*0.4CM
3	MARBLE TILES 40*40*0.4CM
2-SKIRTING	
CODE	
1	CERAMIC 15CM HEIGHT
2	MARBLE 15CM HEIGHT
3-WALL	
CODE	
1	PLASTIC PAINT
2	
4-CEILING	
CODE	
1	PLASTIC PAINT
2	GYPSUM BOARD

DOOR Schedule			
ID	WEADTH	HIGHT	DOORSTILL
1	1.60	2.20	2.20
2	0.90	2.20	2.20
3	1.80	2.20	2.20


WINDOW Schedule				
ID	WEADTH	HIGHT	STILL	WINDOW STILL
1	2.50	1.20	2.20	0.90
2	2.00	1.20	2.20	0.90


Youssef Hesham

52010801

checked by: Dr.Abdelrahman

Scale 1/100

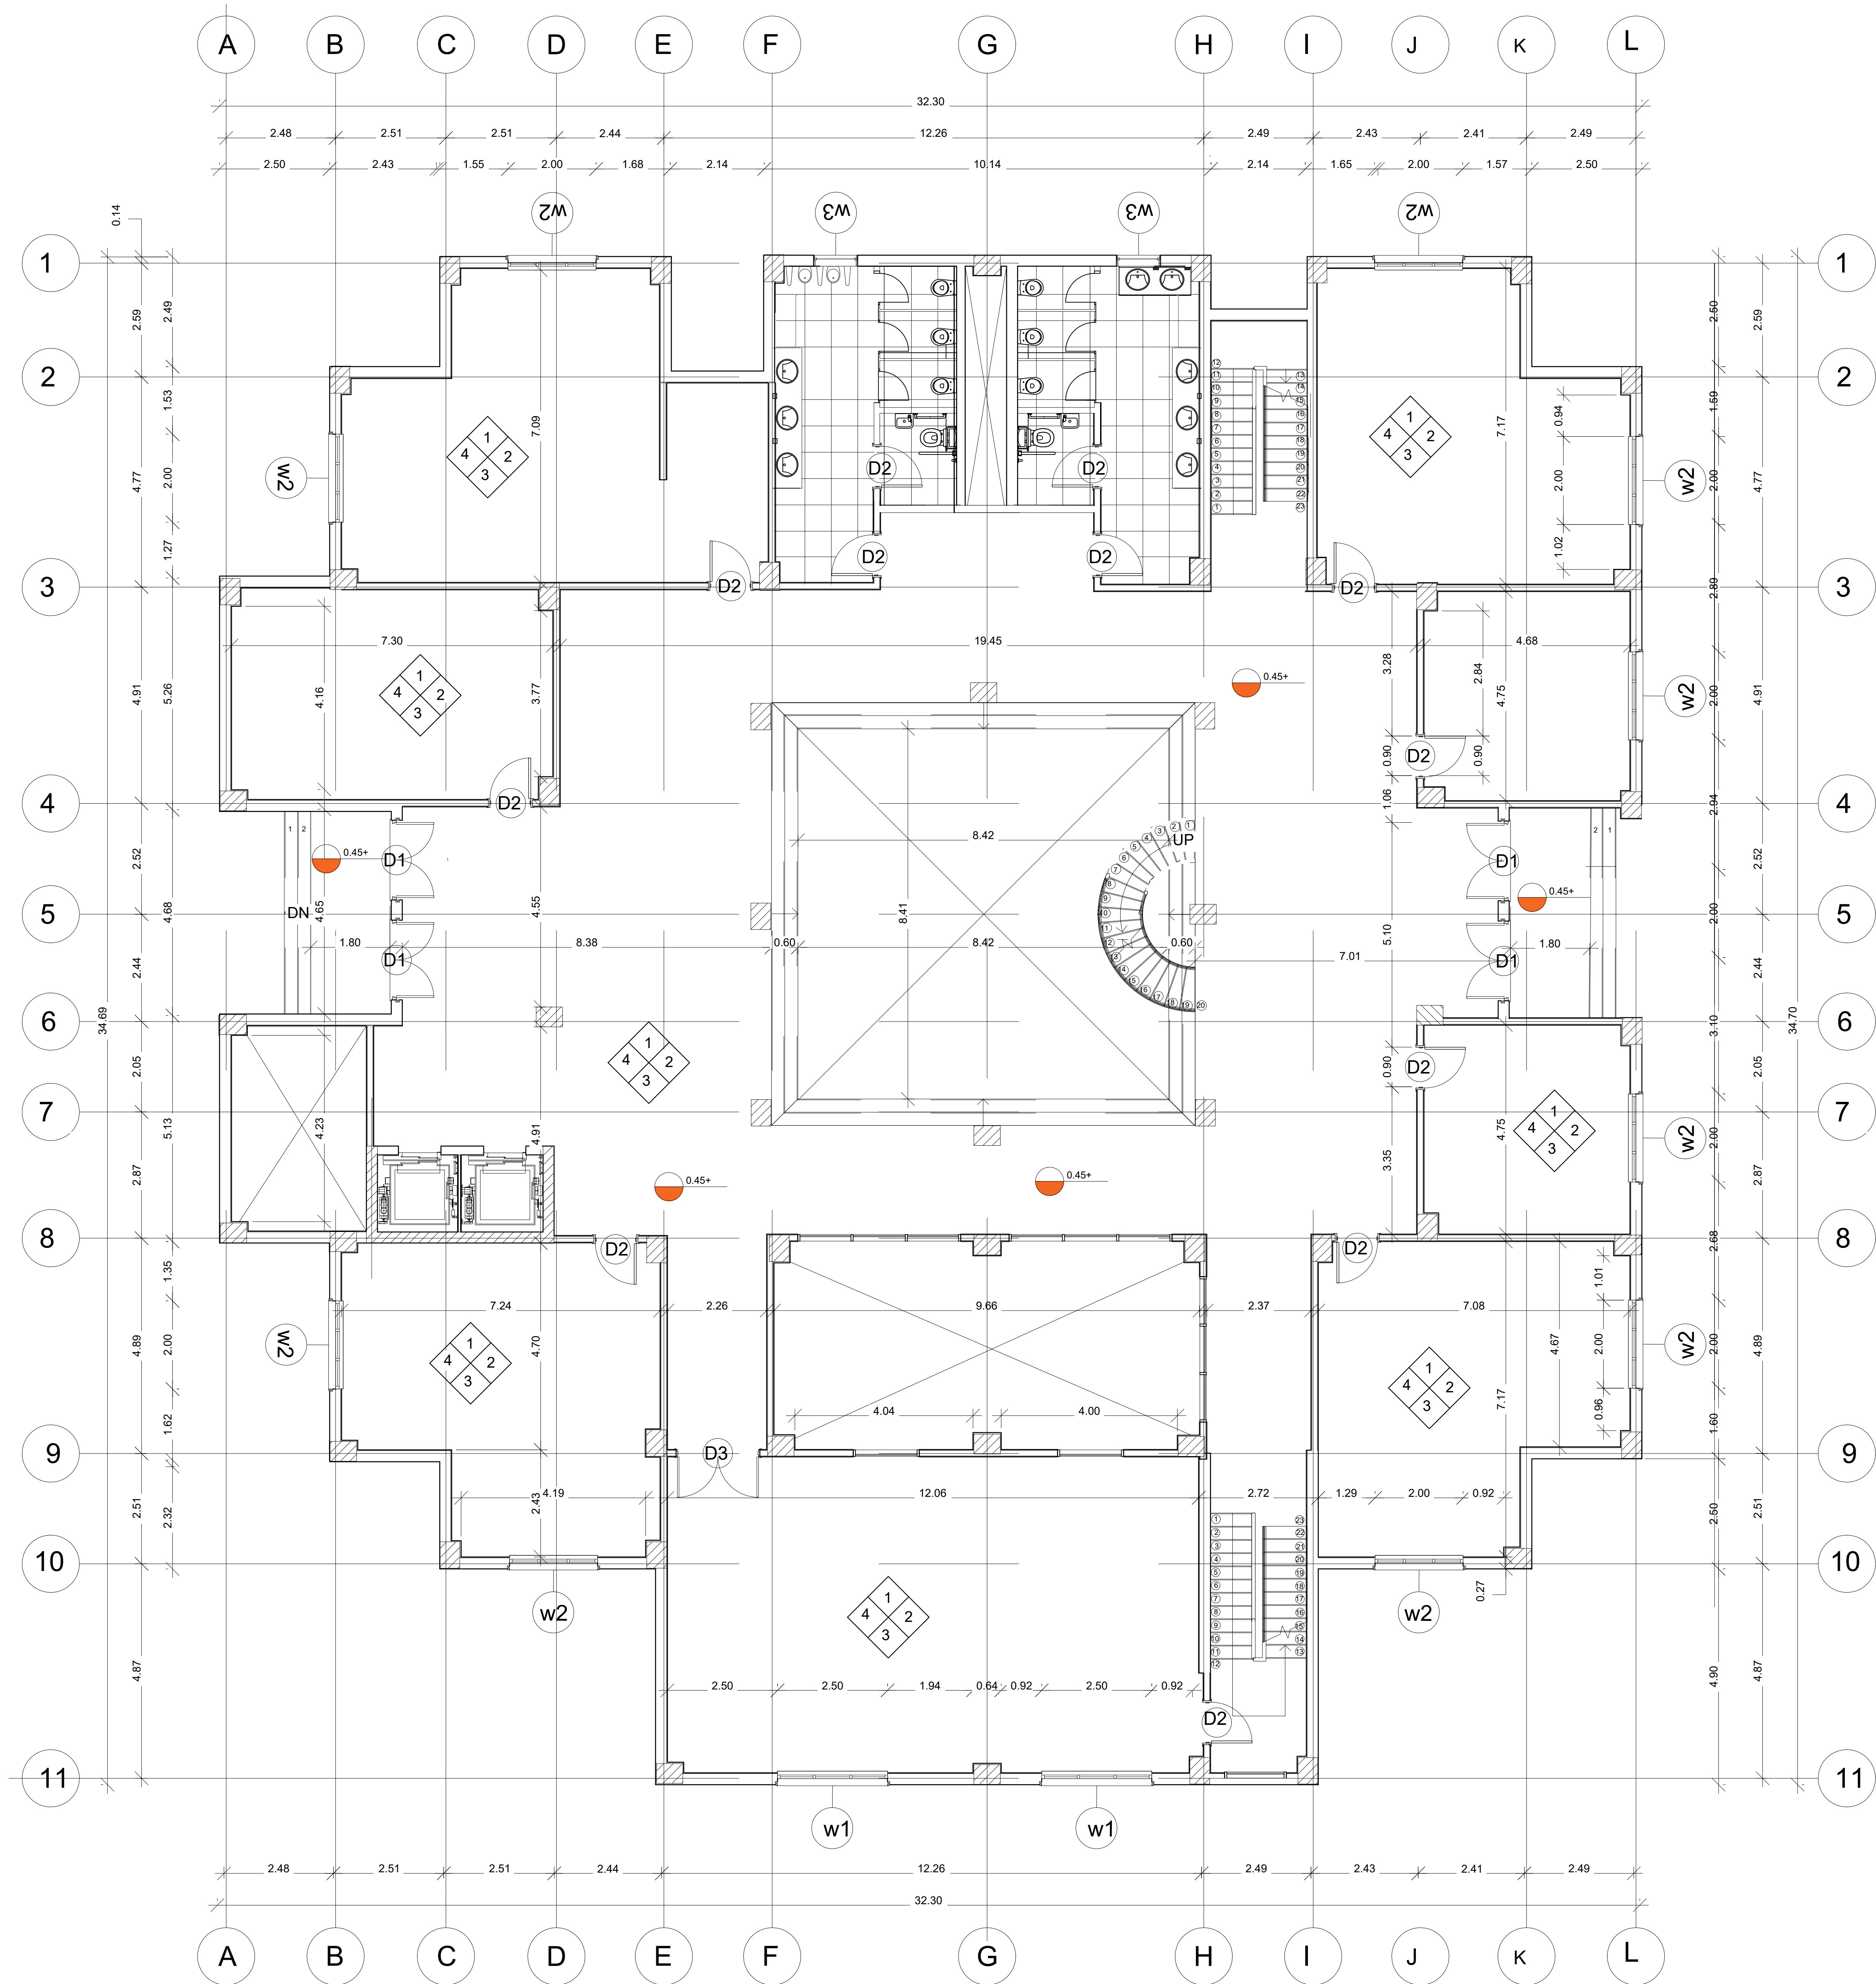

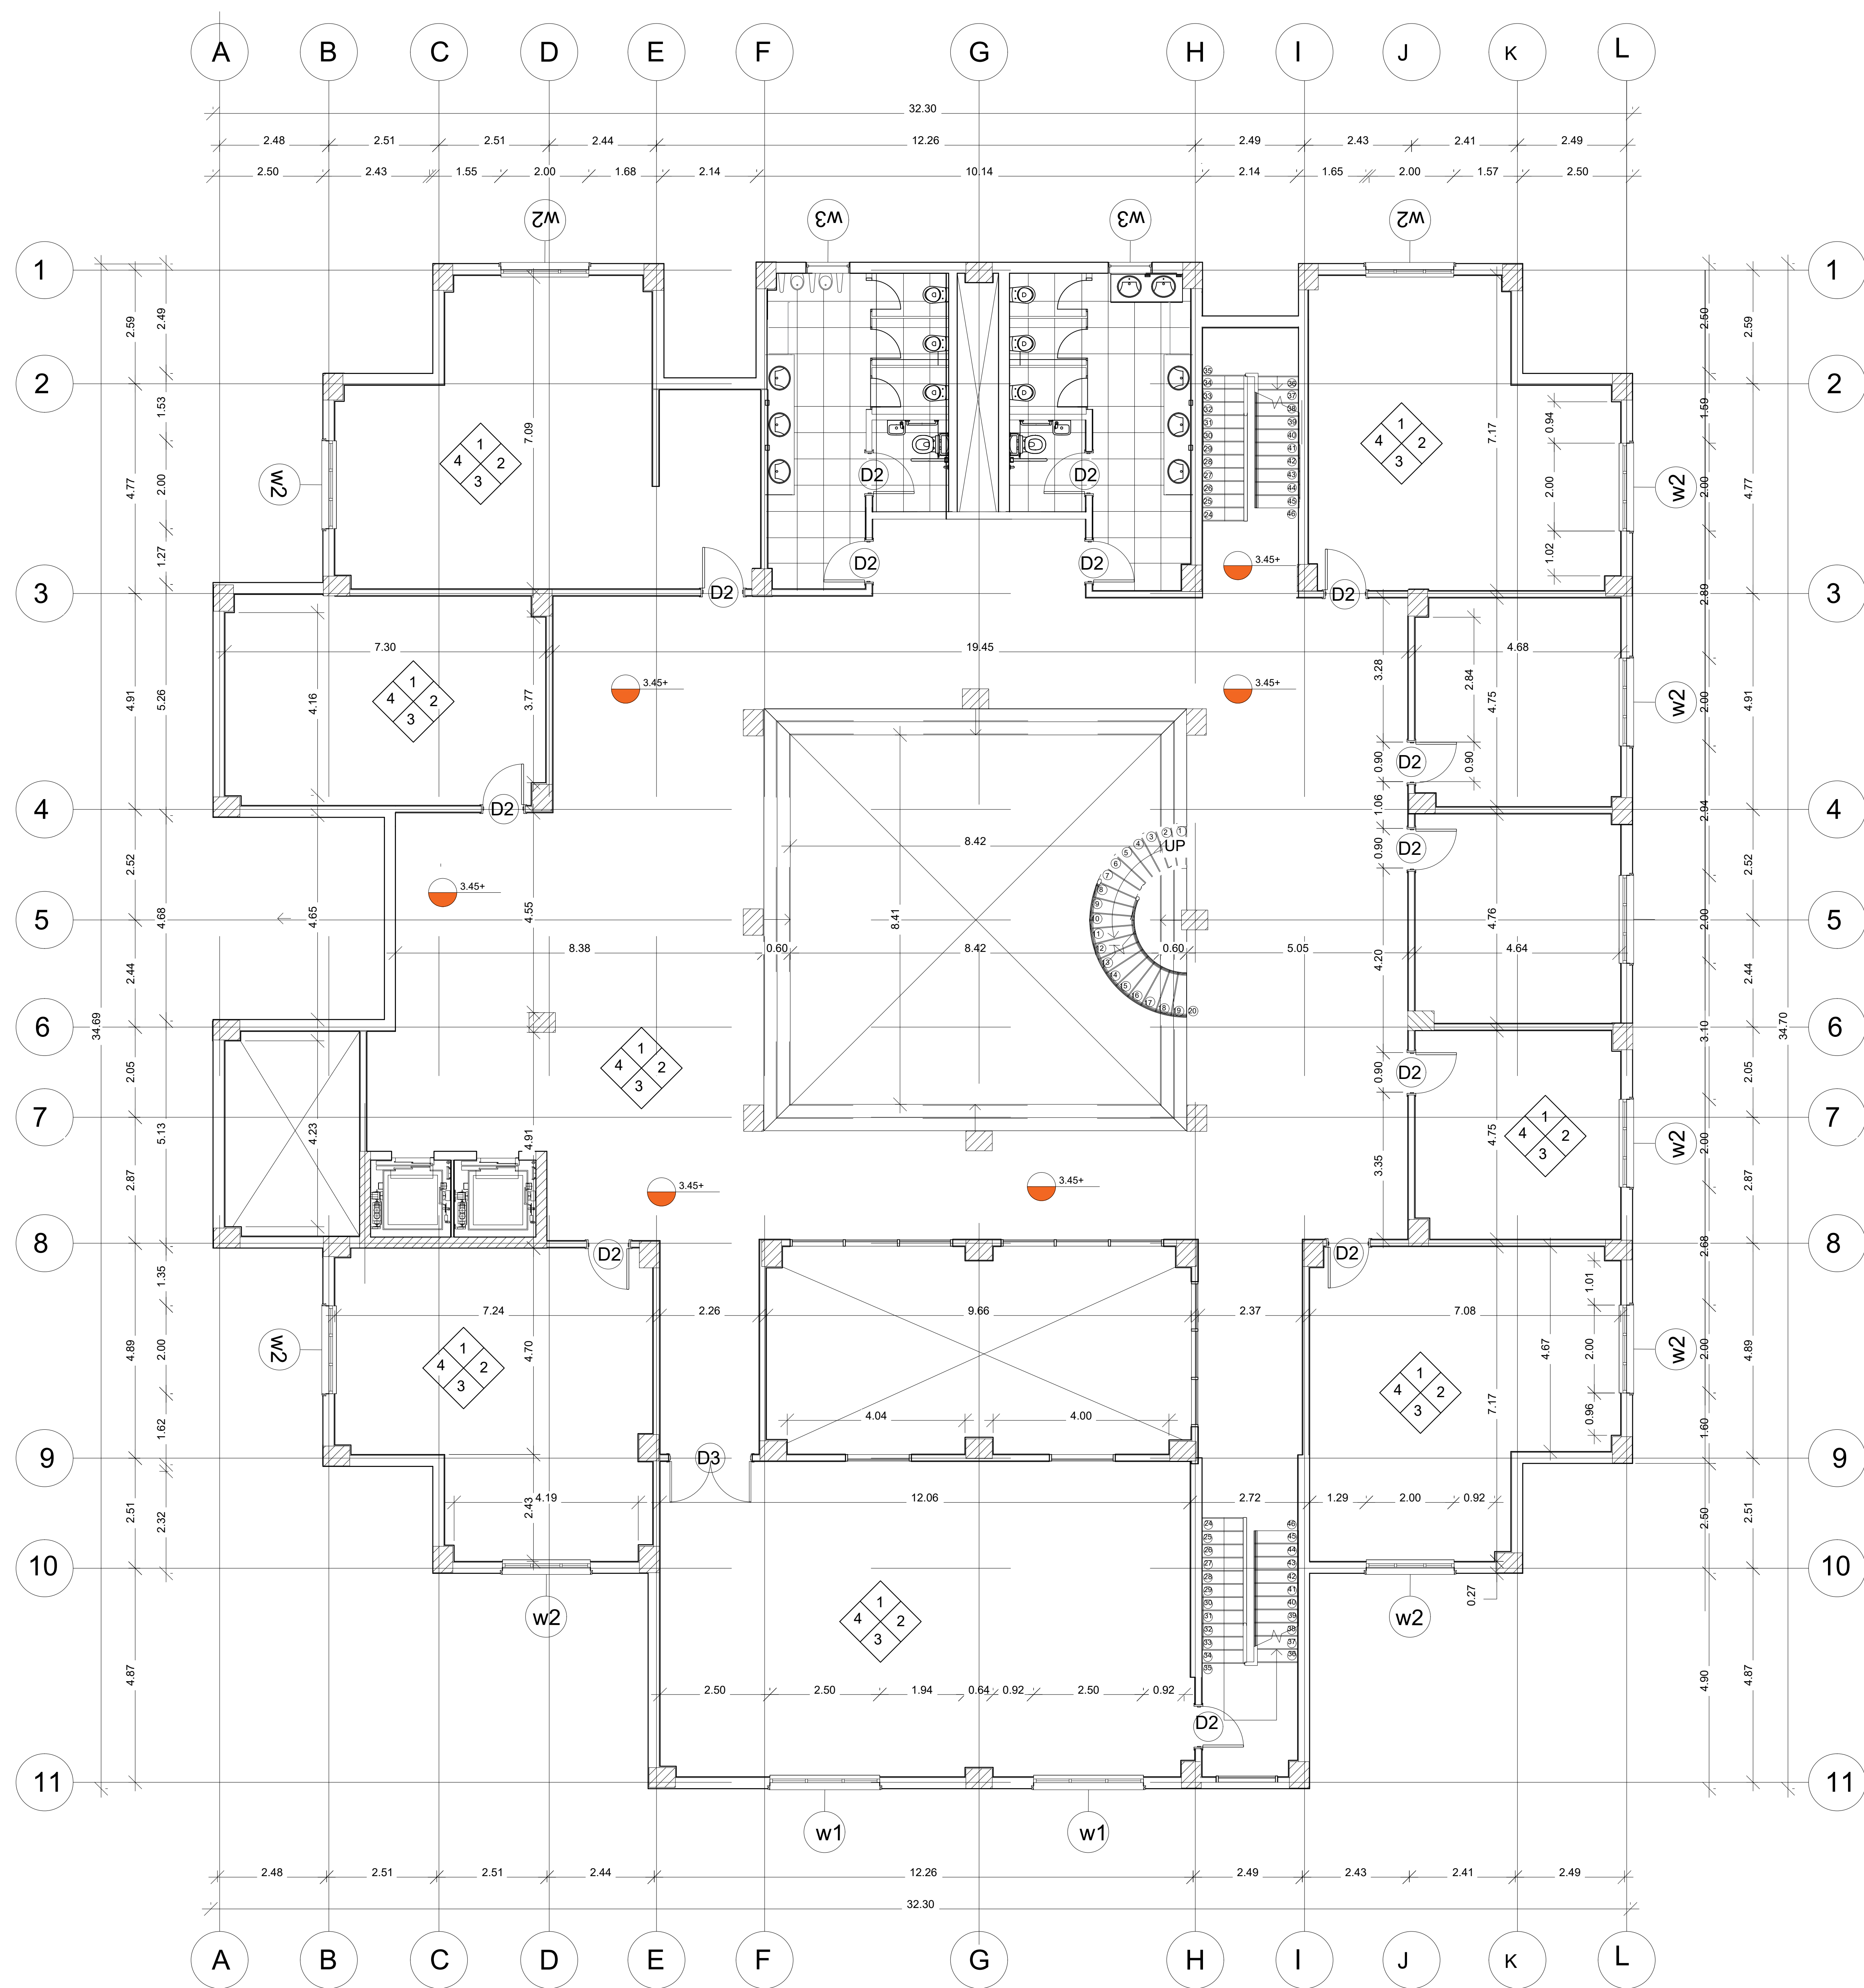

FINSHING Schedule

1-FLOORING	
CODE	
1	CERAMIC TILES 40*40*0.4CM
2	CERAMIC TILES 20*20*0.4CM
3	MARBLE TILES 40*40*0.4CM
2-SKIRTING	
CODE	
1	CERAMIC 15CM HEIGHT
2	MARBLE 15CM HEIGHT
3-WALL	
CODE	
1	PLASTIC PAINT
2	
4-CEILING	
CODE	
1	PLASTIC PAINT
2	GYPSUM BOARD

DOOR Schedule			
ID	WEADTH	HIGHT	DOORSTILL
1	1.60	2.20	2.20
2	0.90	2.20	2.20
3	1.80	2.20	2.20


WINDOW Schedule				
ID	WEADTH	HIGHT	STILL	WINDOW STILL
1	2.50	1.20	2.20	0.90
2	2.00	1.20	2.20	0.90

Youssef Hesham

52010801

checked by: Dr.Abdelrahman

Scale 1/100

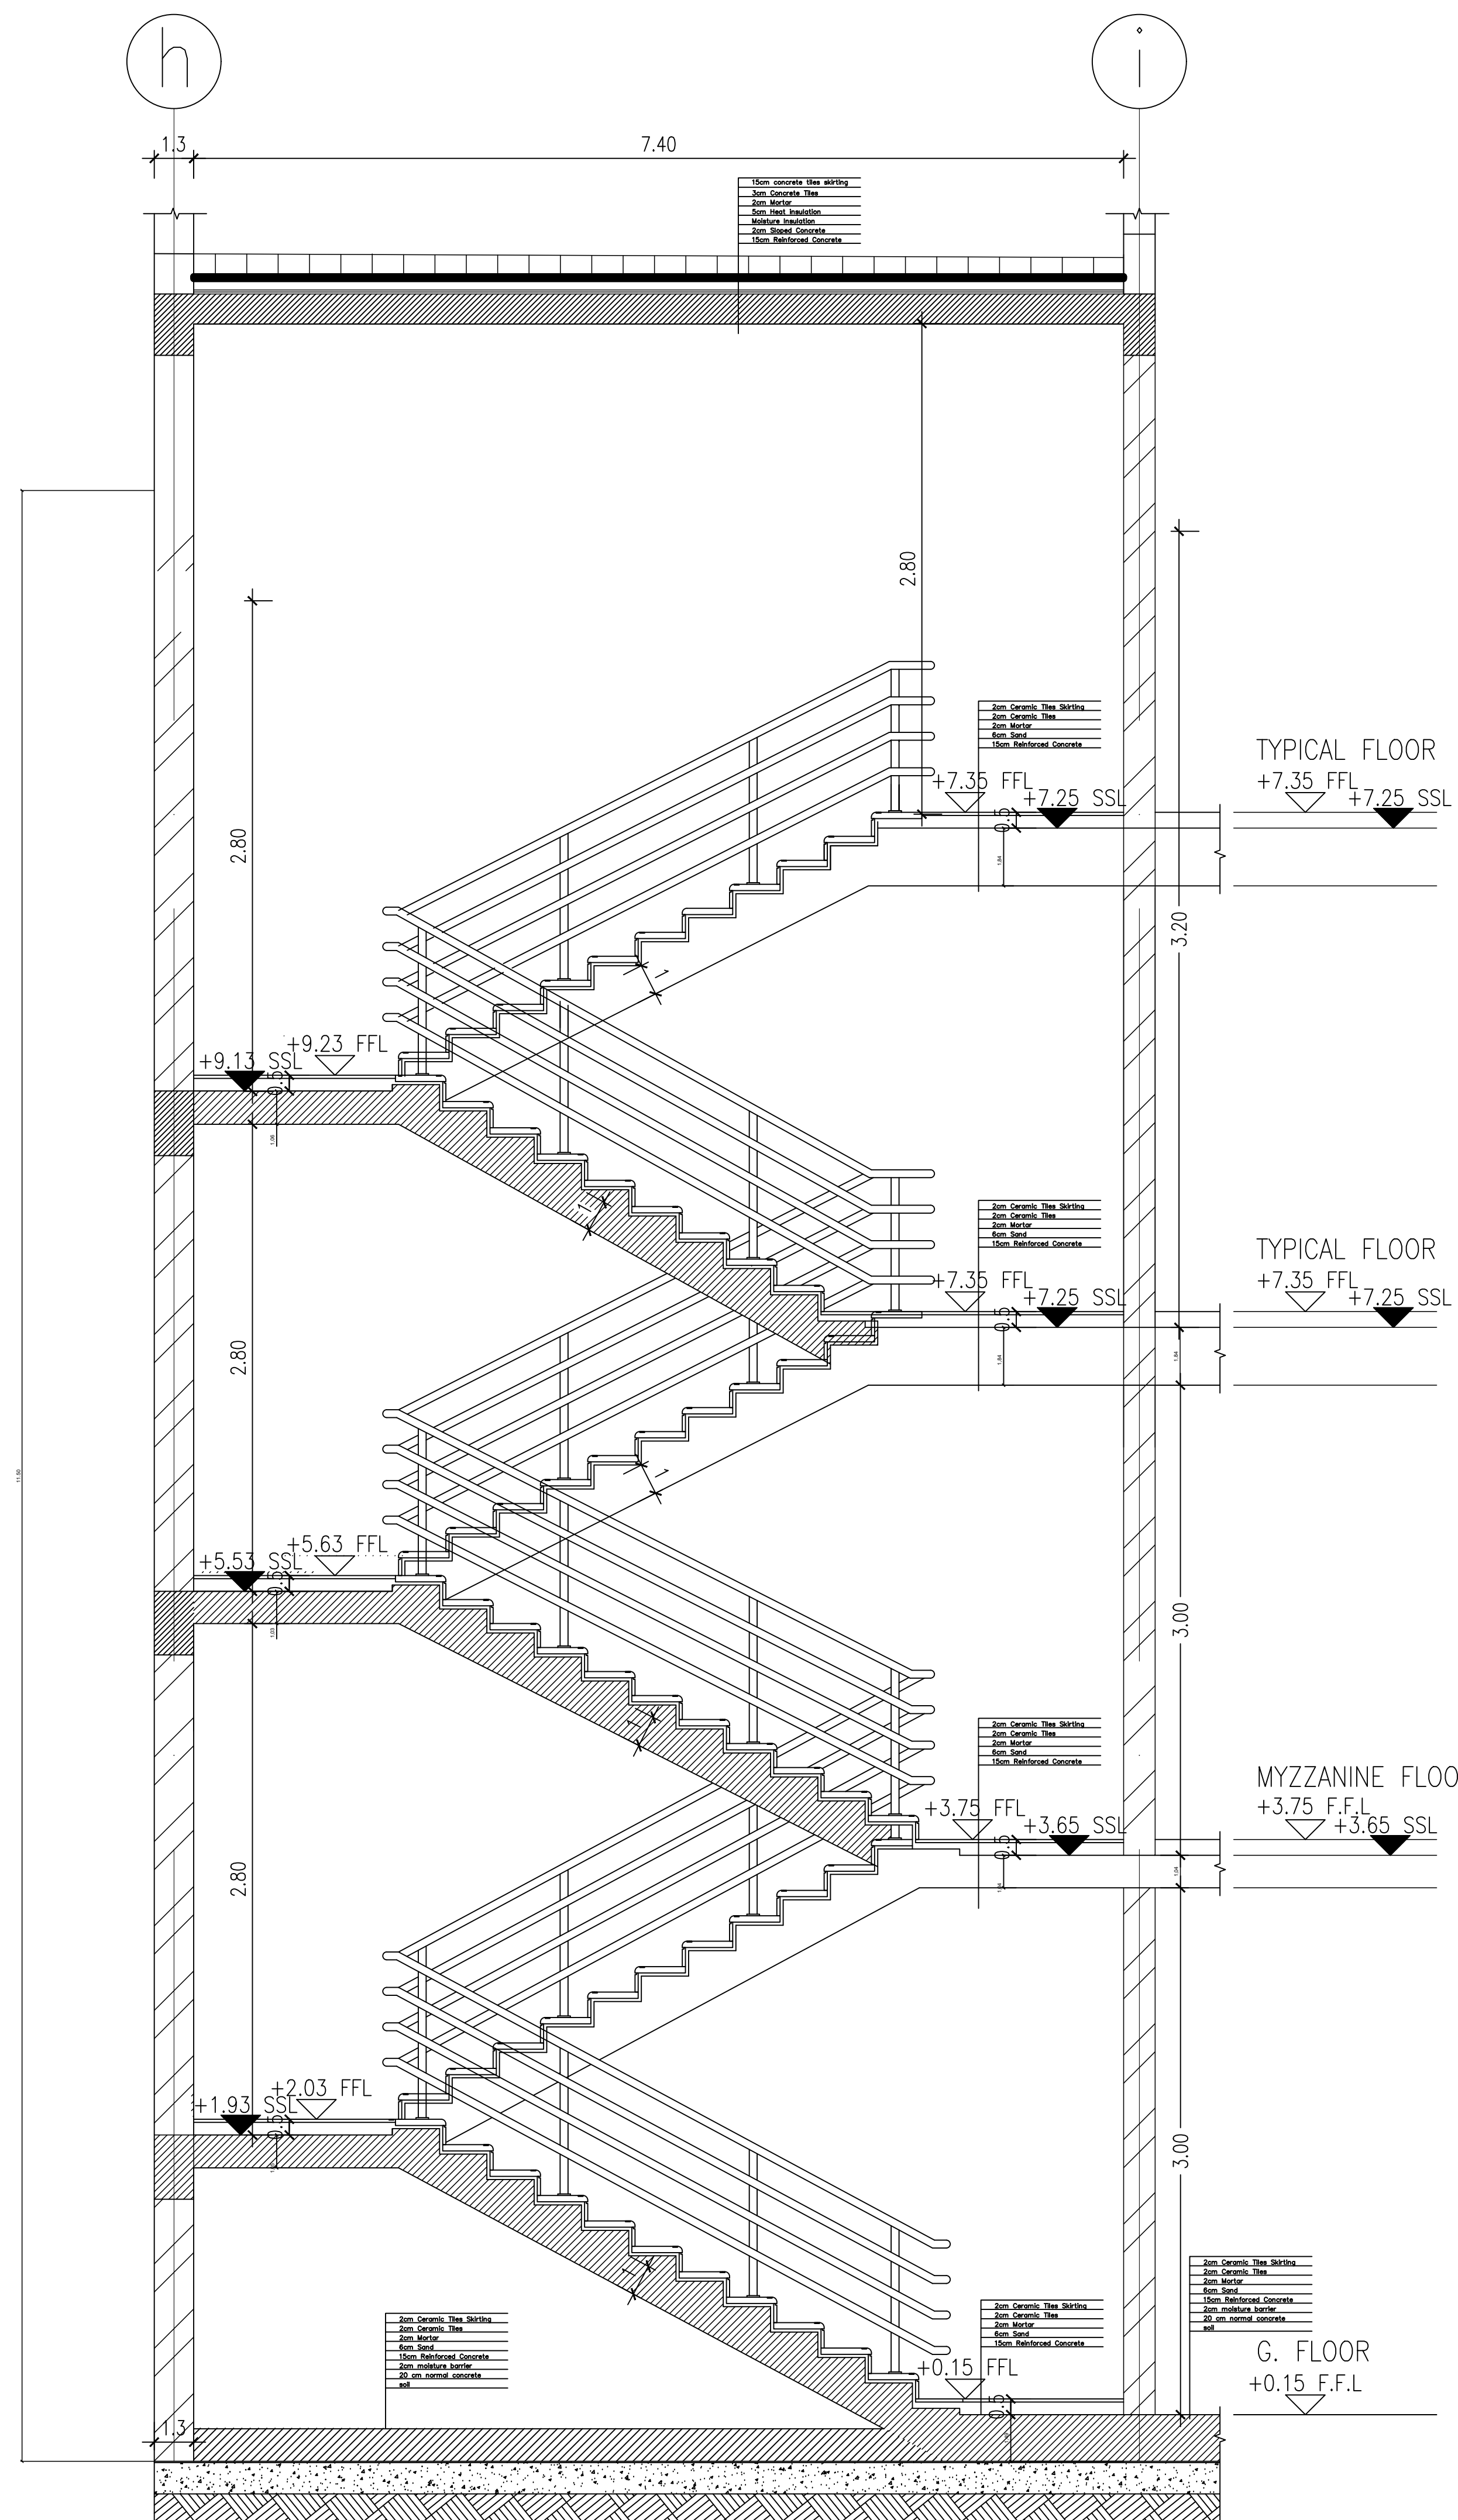

scale 1:20

drawn by: youssef hesham 52010801

checked by: Dr.Abdulrahman

Date	19/8/2024
------	-----------

Stairs section 1:20

Stairs plan 1:20

elevator plan 1:20

Stairs plan 1:20

working 3



```
scale 1:20
```

drawn by: youssef hesham 52010801

checked by: Dr.Abdulrahman

Date 29/7/2024

Stairs & elevator
plans

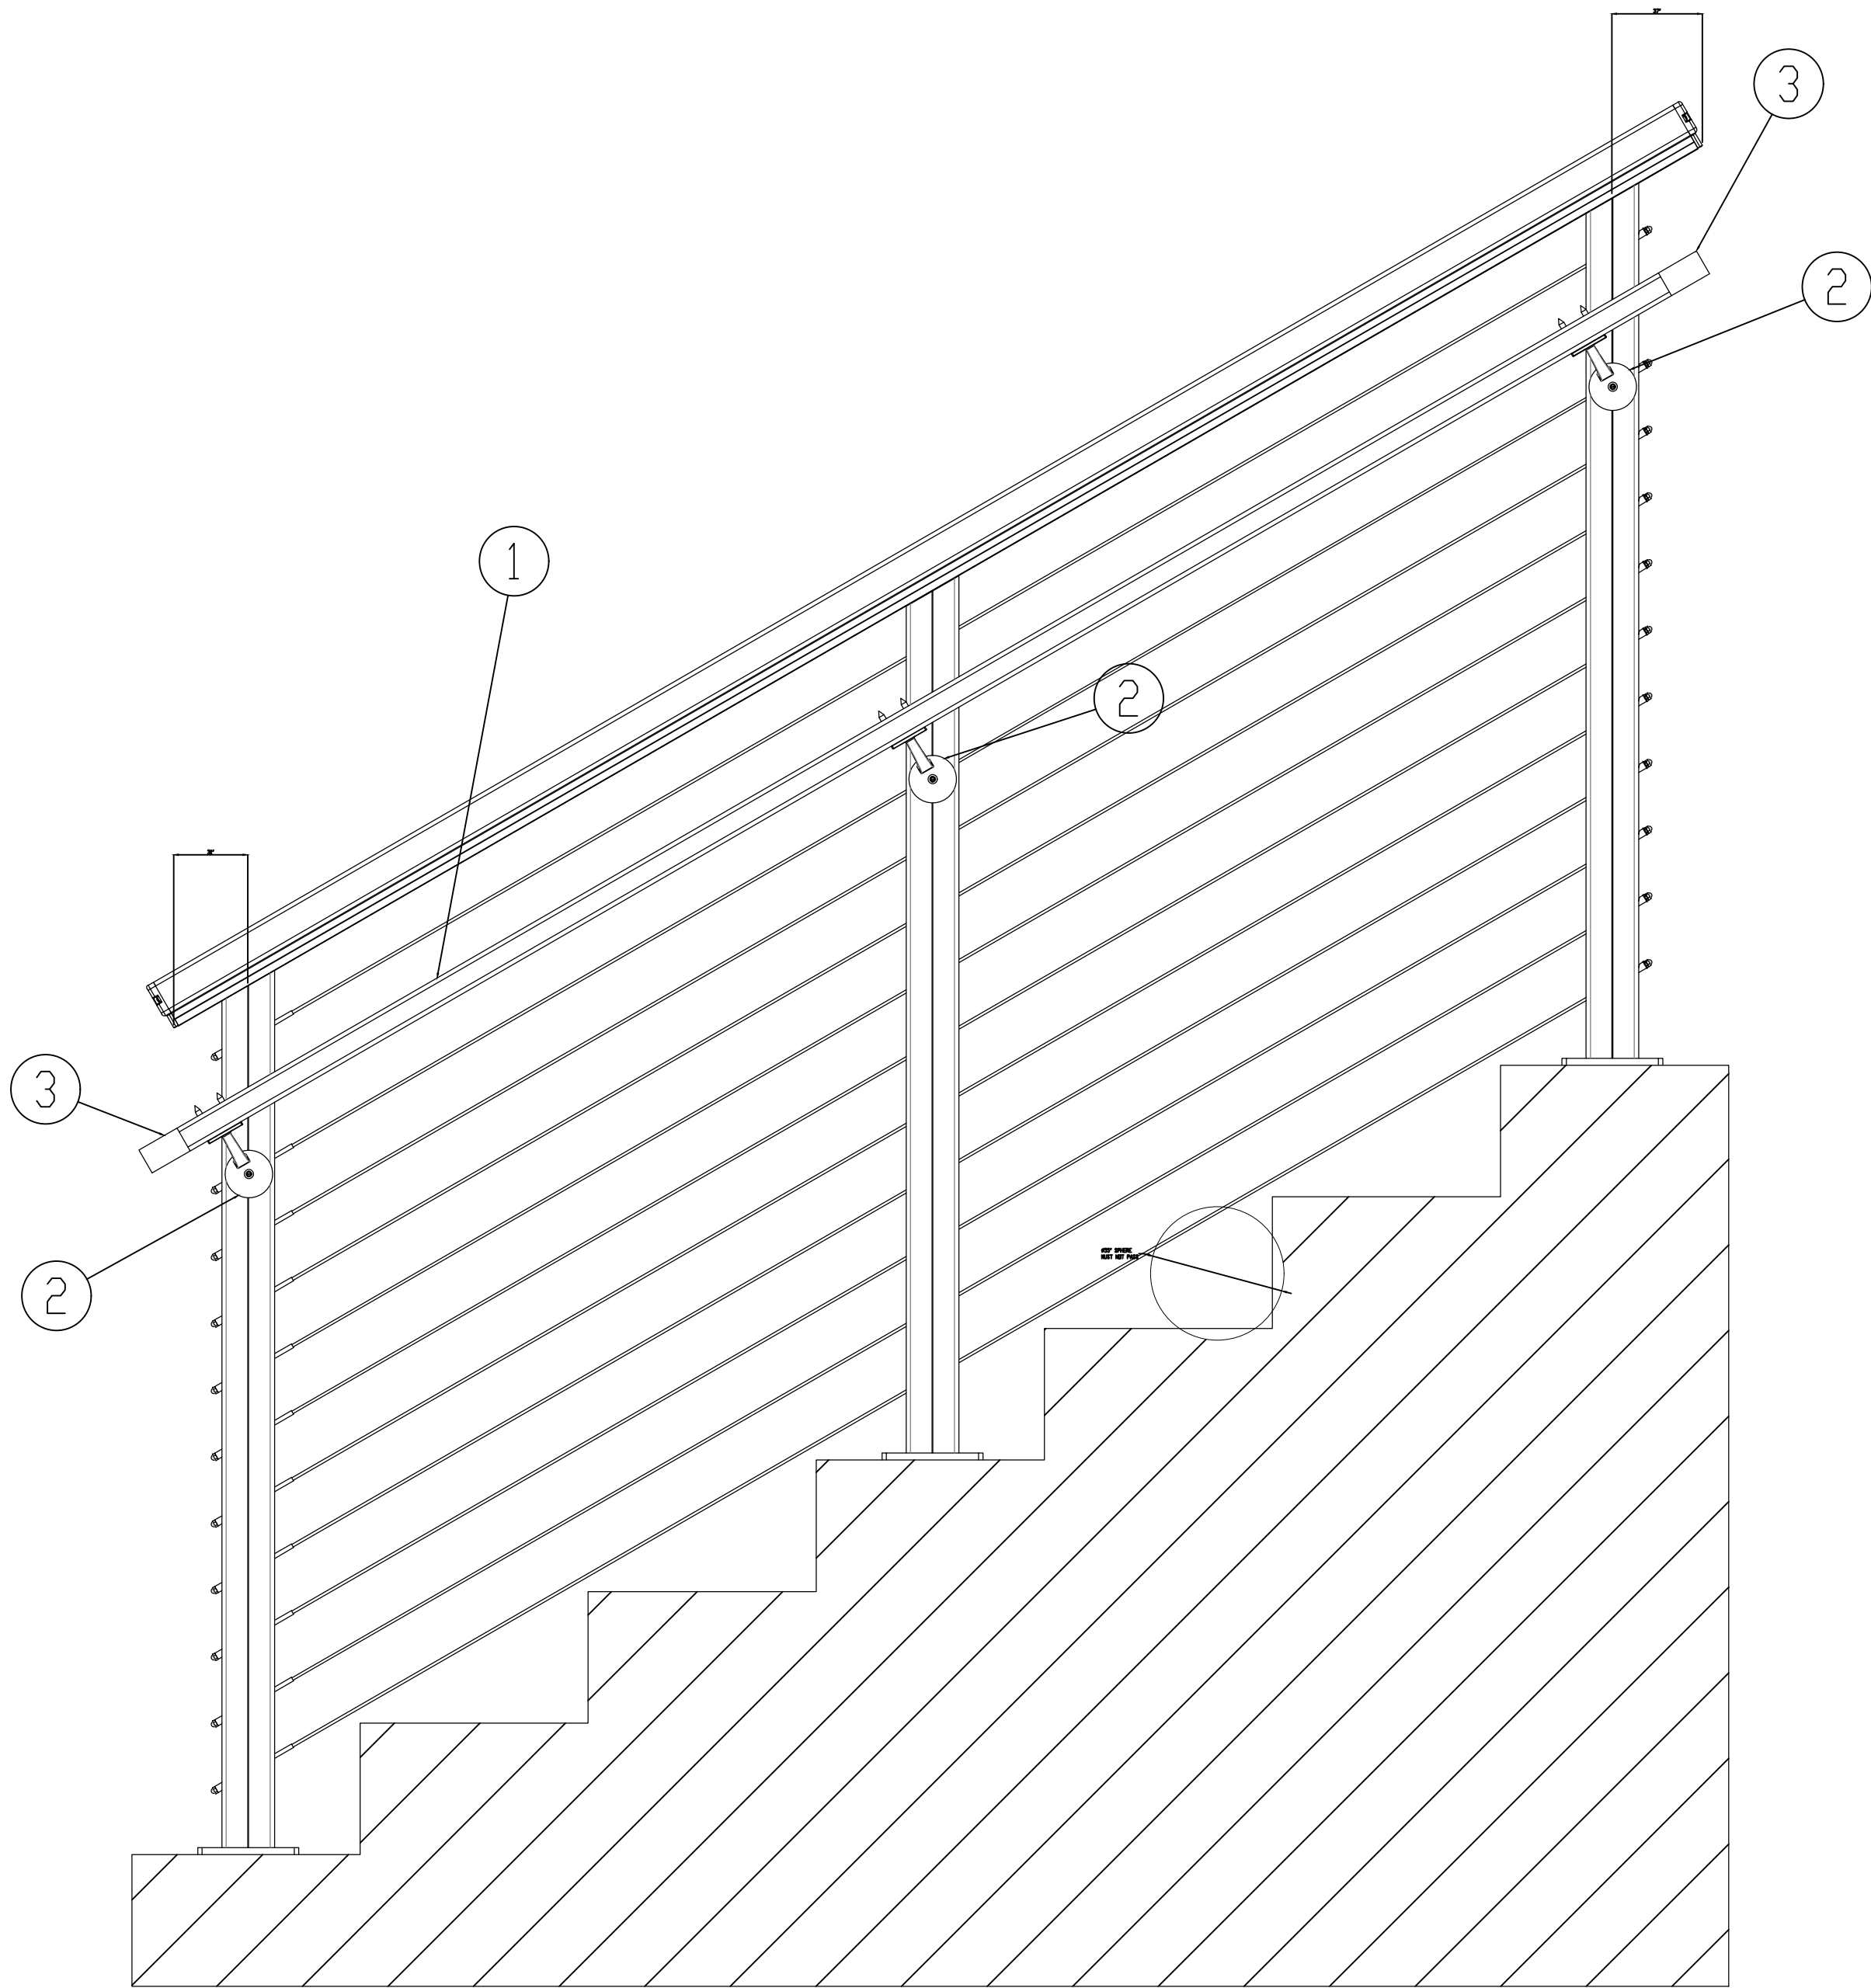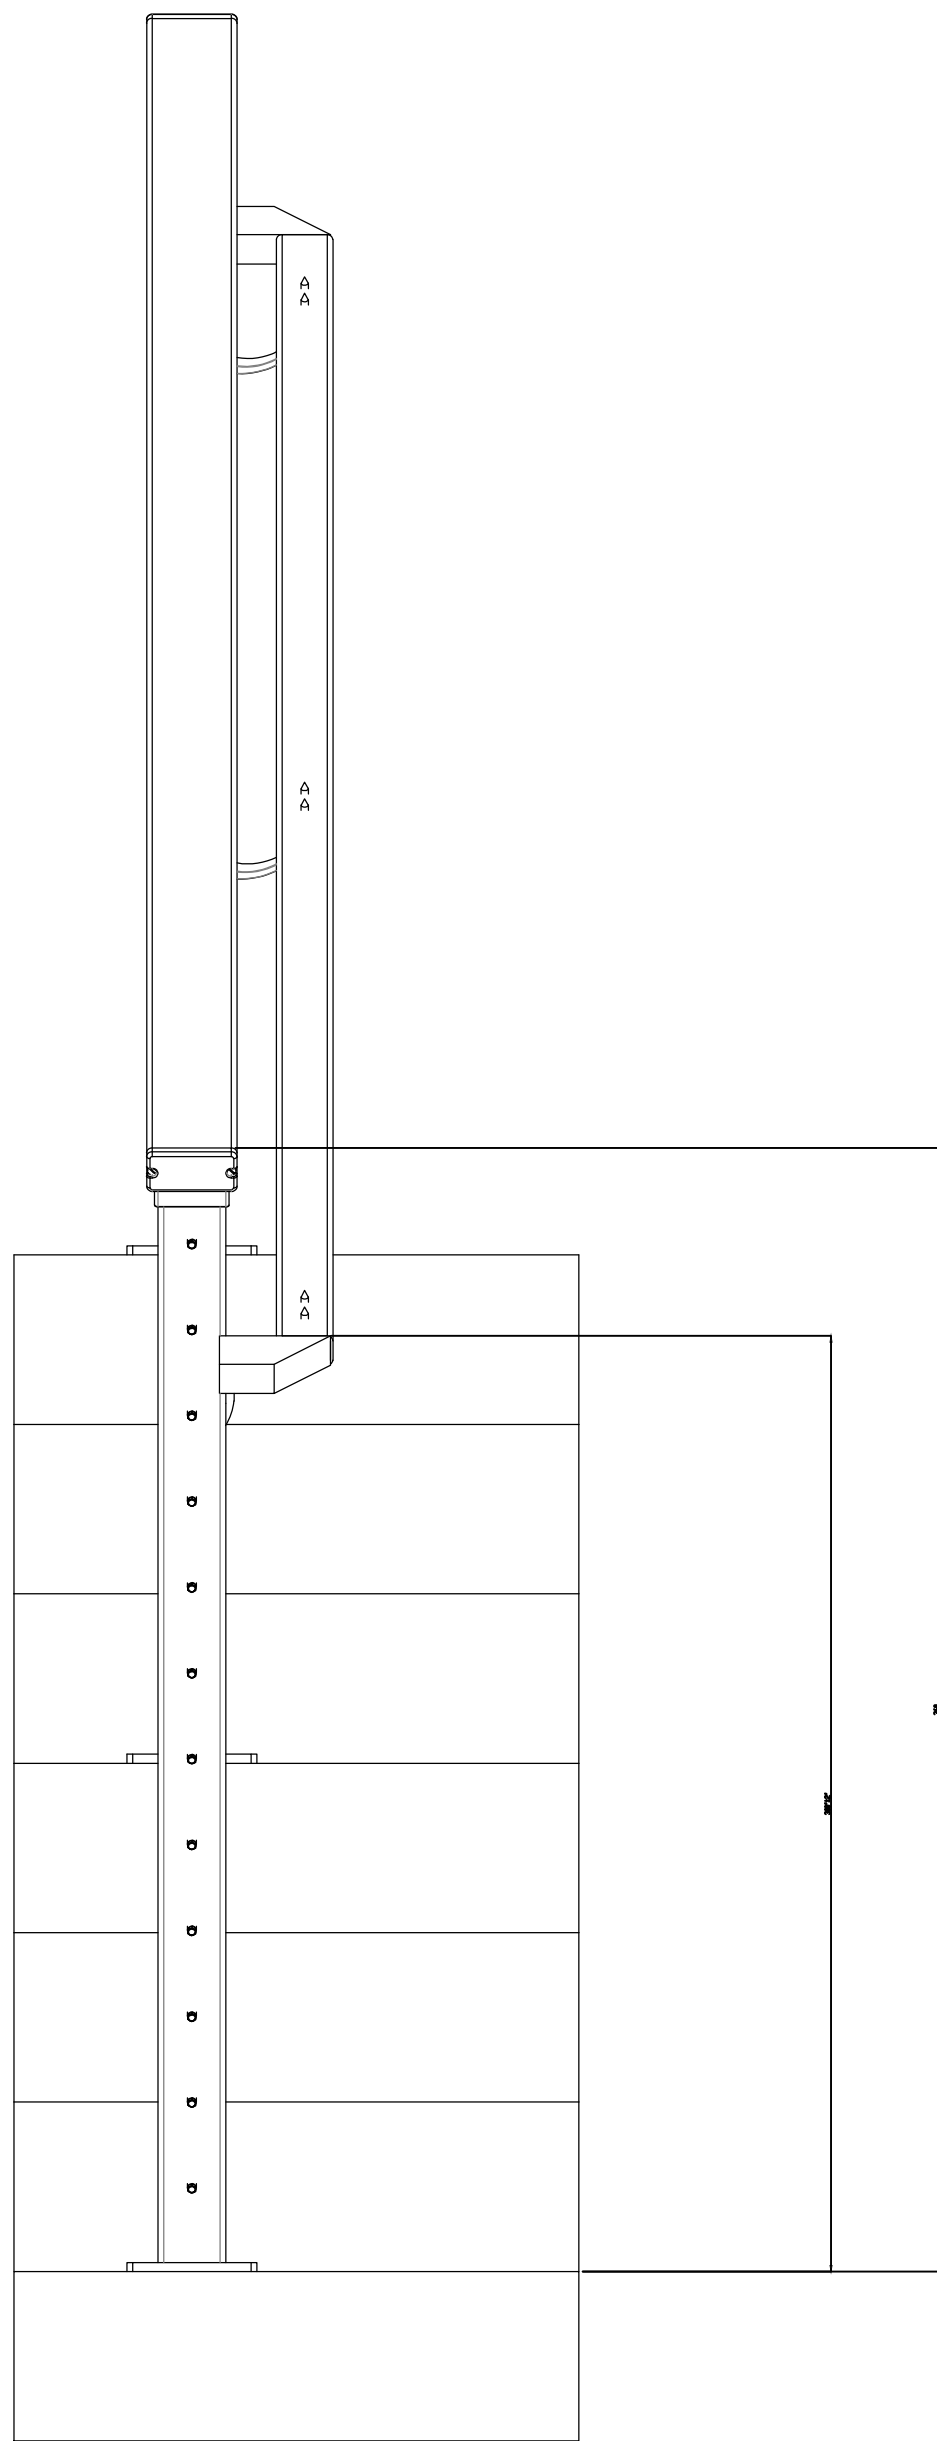

working
3

Youssef Hesham
52010801


checked by:
Dr.Abdelrahman

Date:
19/8/2024


Scale

1:5

ITEM NO.	DESCRIPTION	QTY.
1	POST-TO-POST	1
2	POST-TO-POST HANDRAIL BRACKET	3
3	POST TO POST WALL RETURN	2

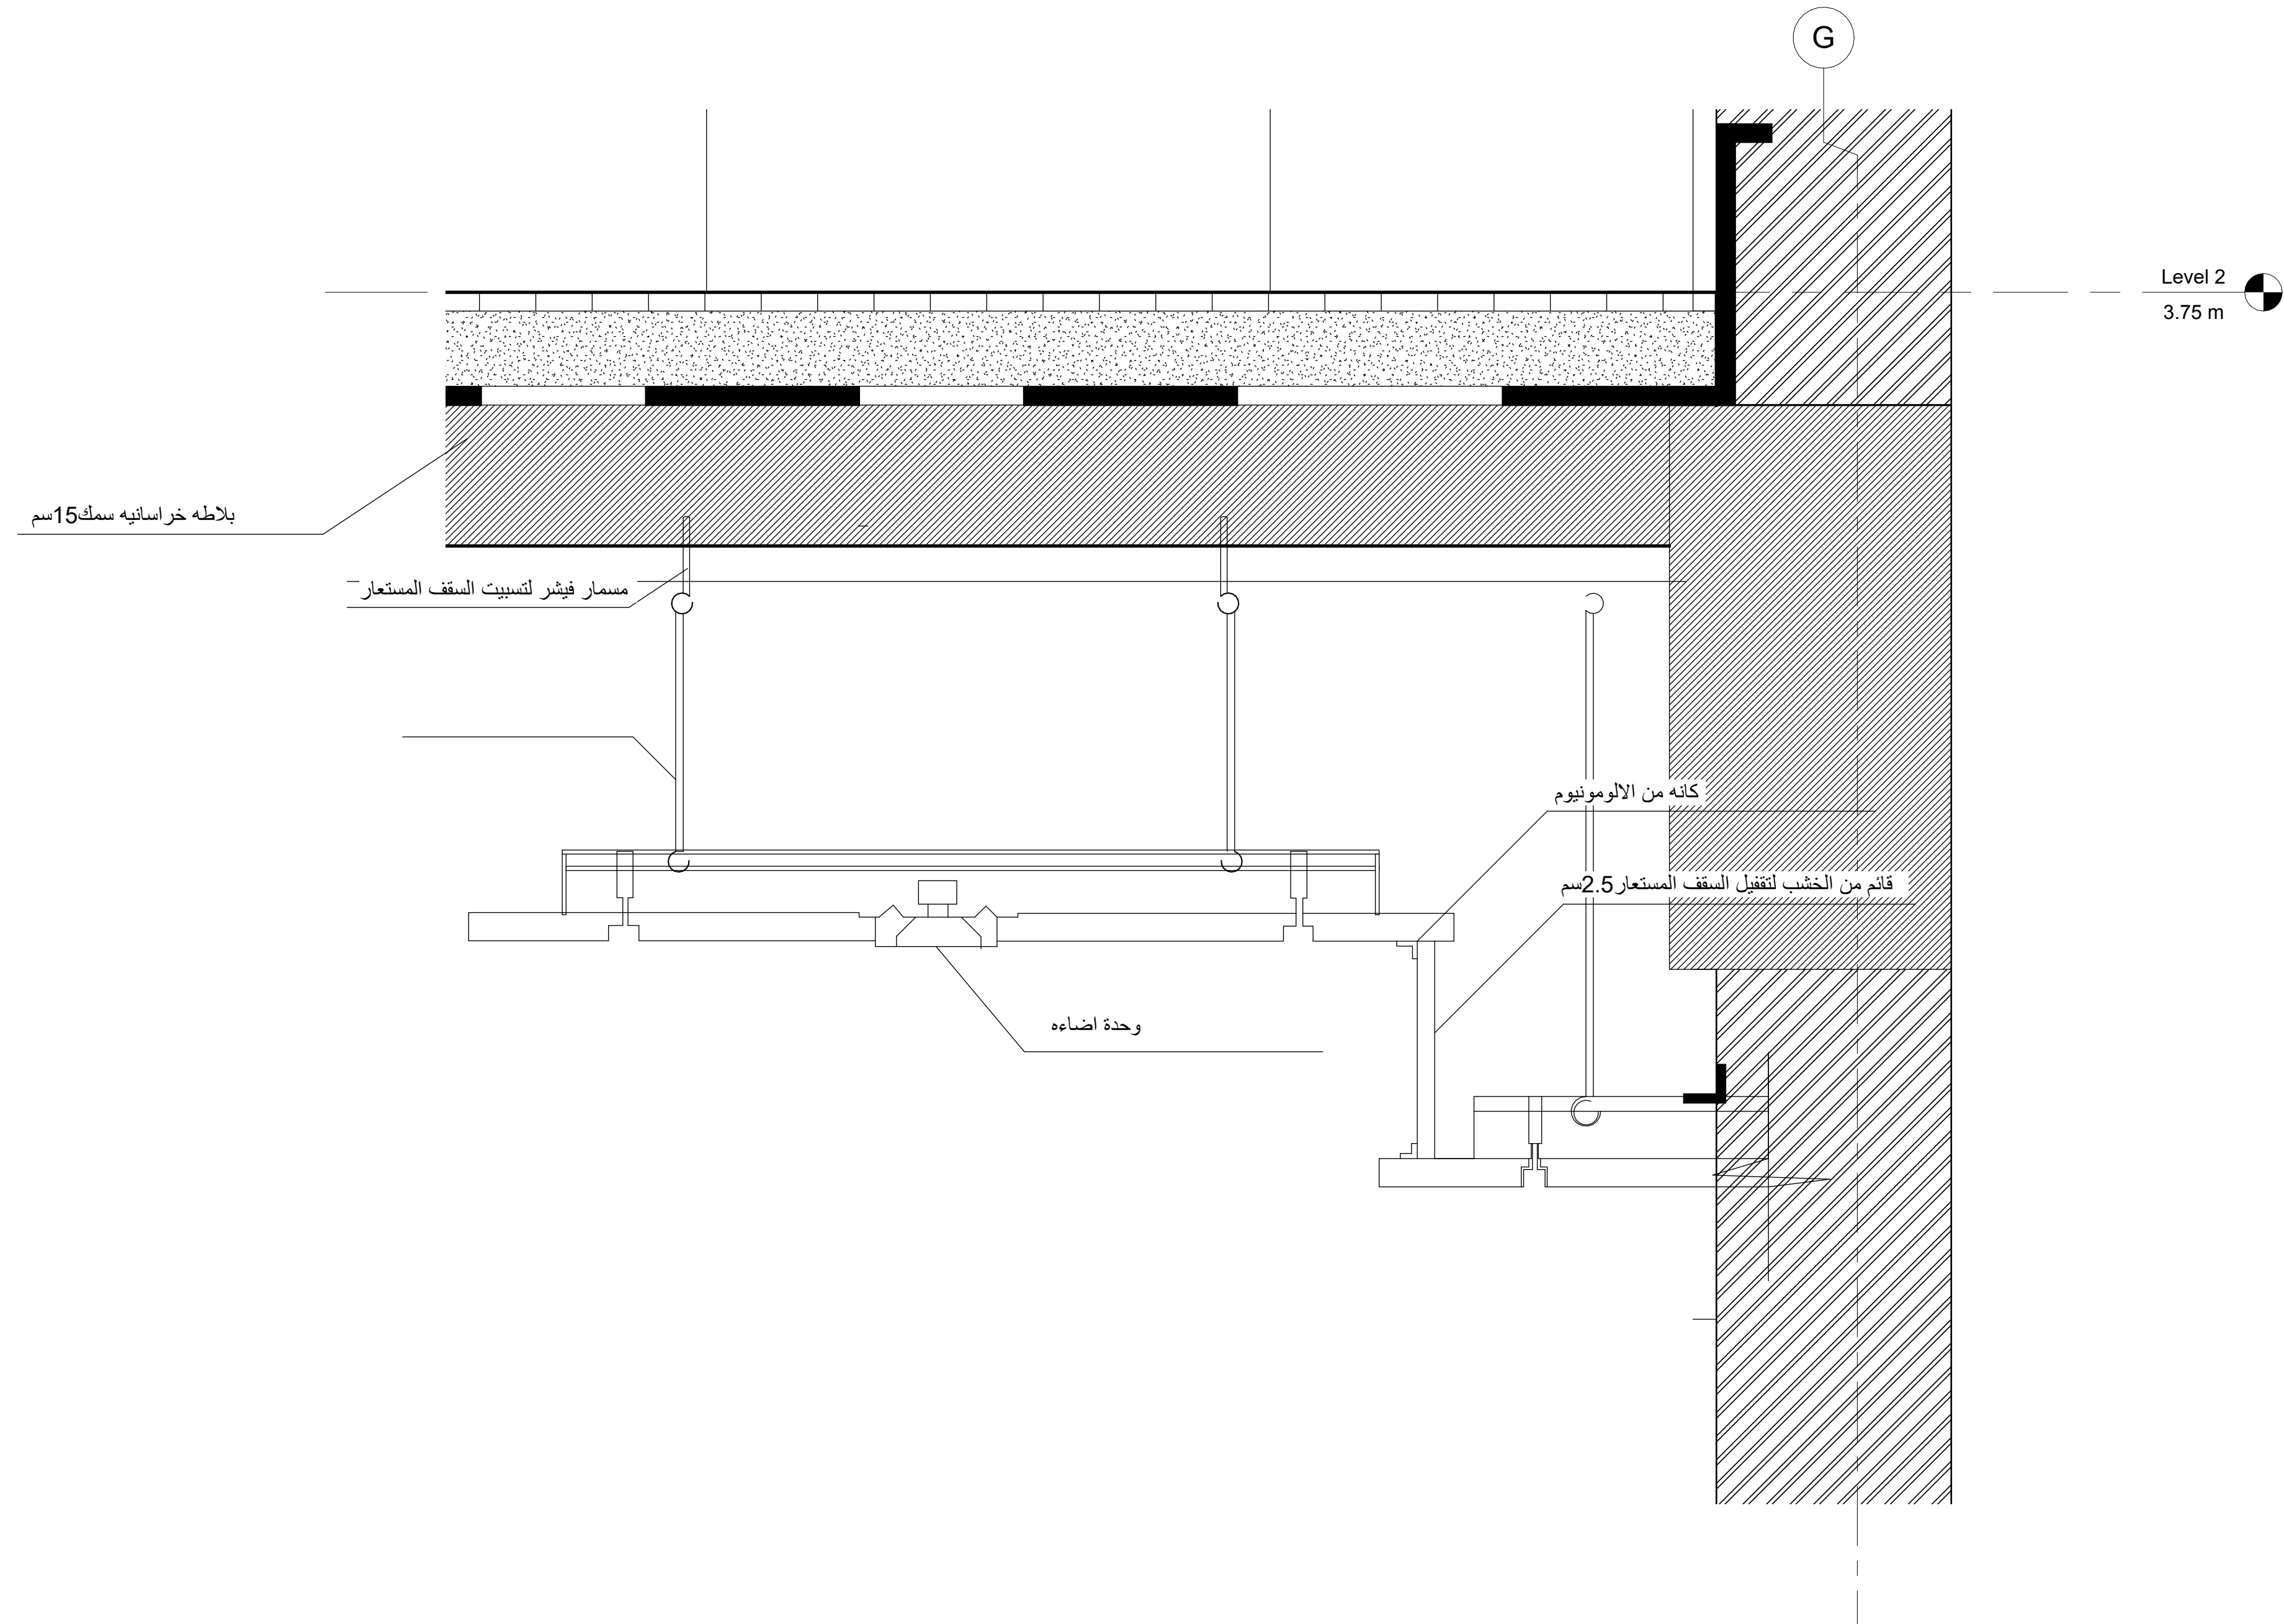

1 Section 1 - Callout 2
1 : 5

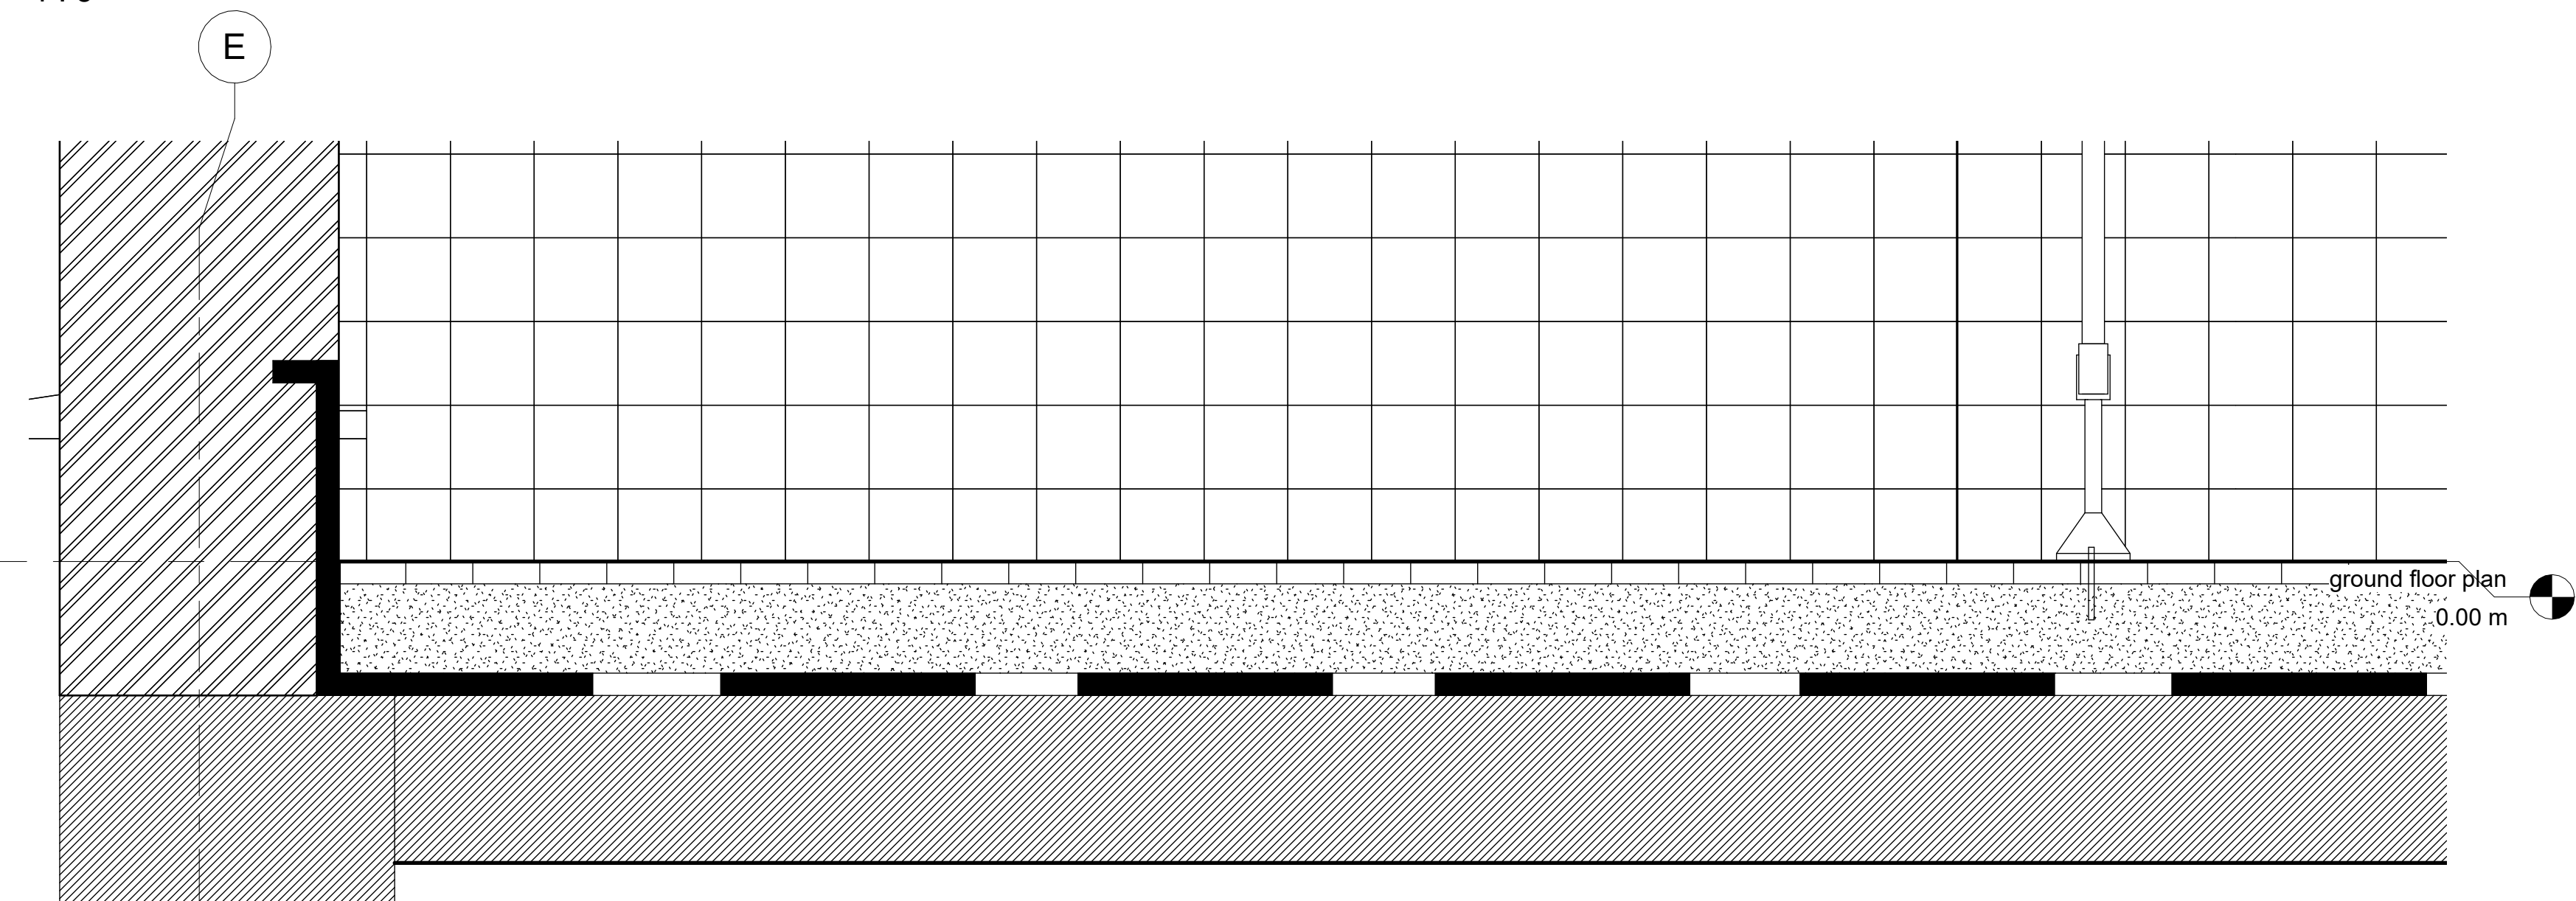

2 Section 1 - Callout 1
1 : 5

WORKING 3 DETAILS

SCALE 1:5

Date 3/8/2024

checked by: Dr.abdulrahman

drawn by: youssef hesham

52010801



1	marble floors (Black and white)
2	Black Spanish Marble 45*45
3	3) MDF FLOORING 30CM* 60CM
4	4) Ceramic 50cm*50cm


Youssef Hesham

52010801


checked by: Dr.Abdelrahman

Scale 1/100

ارضيات

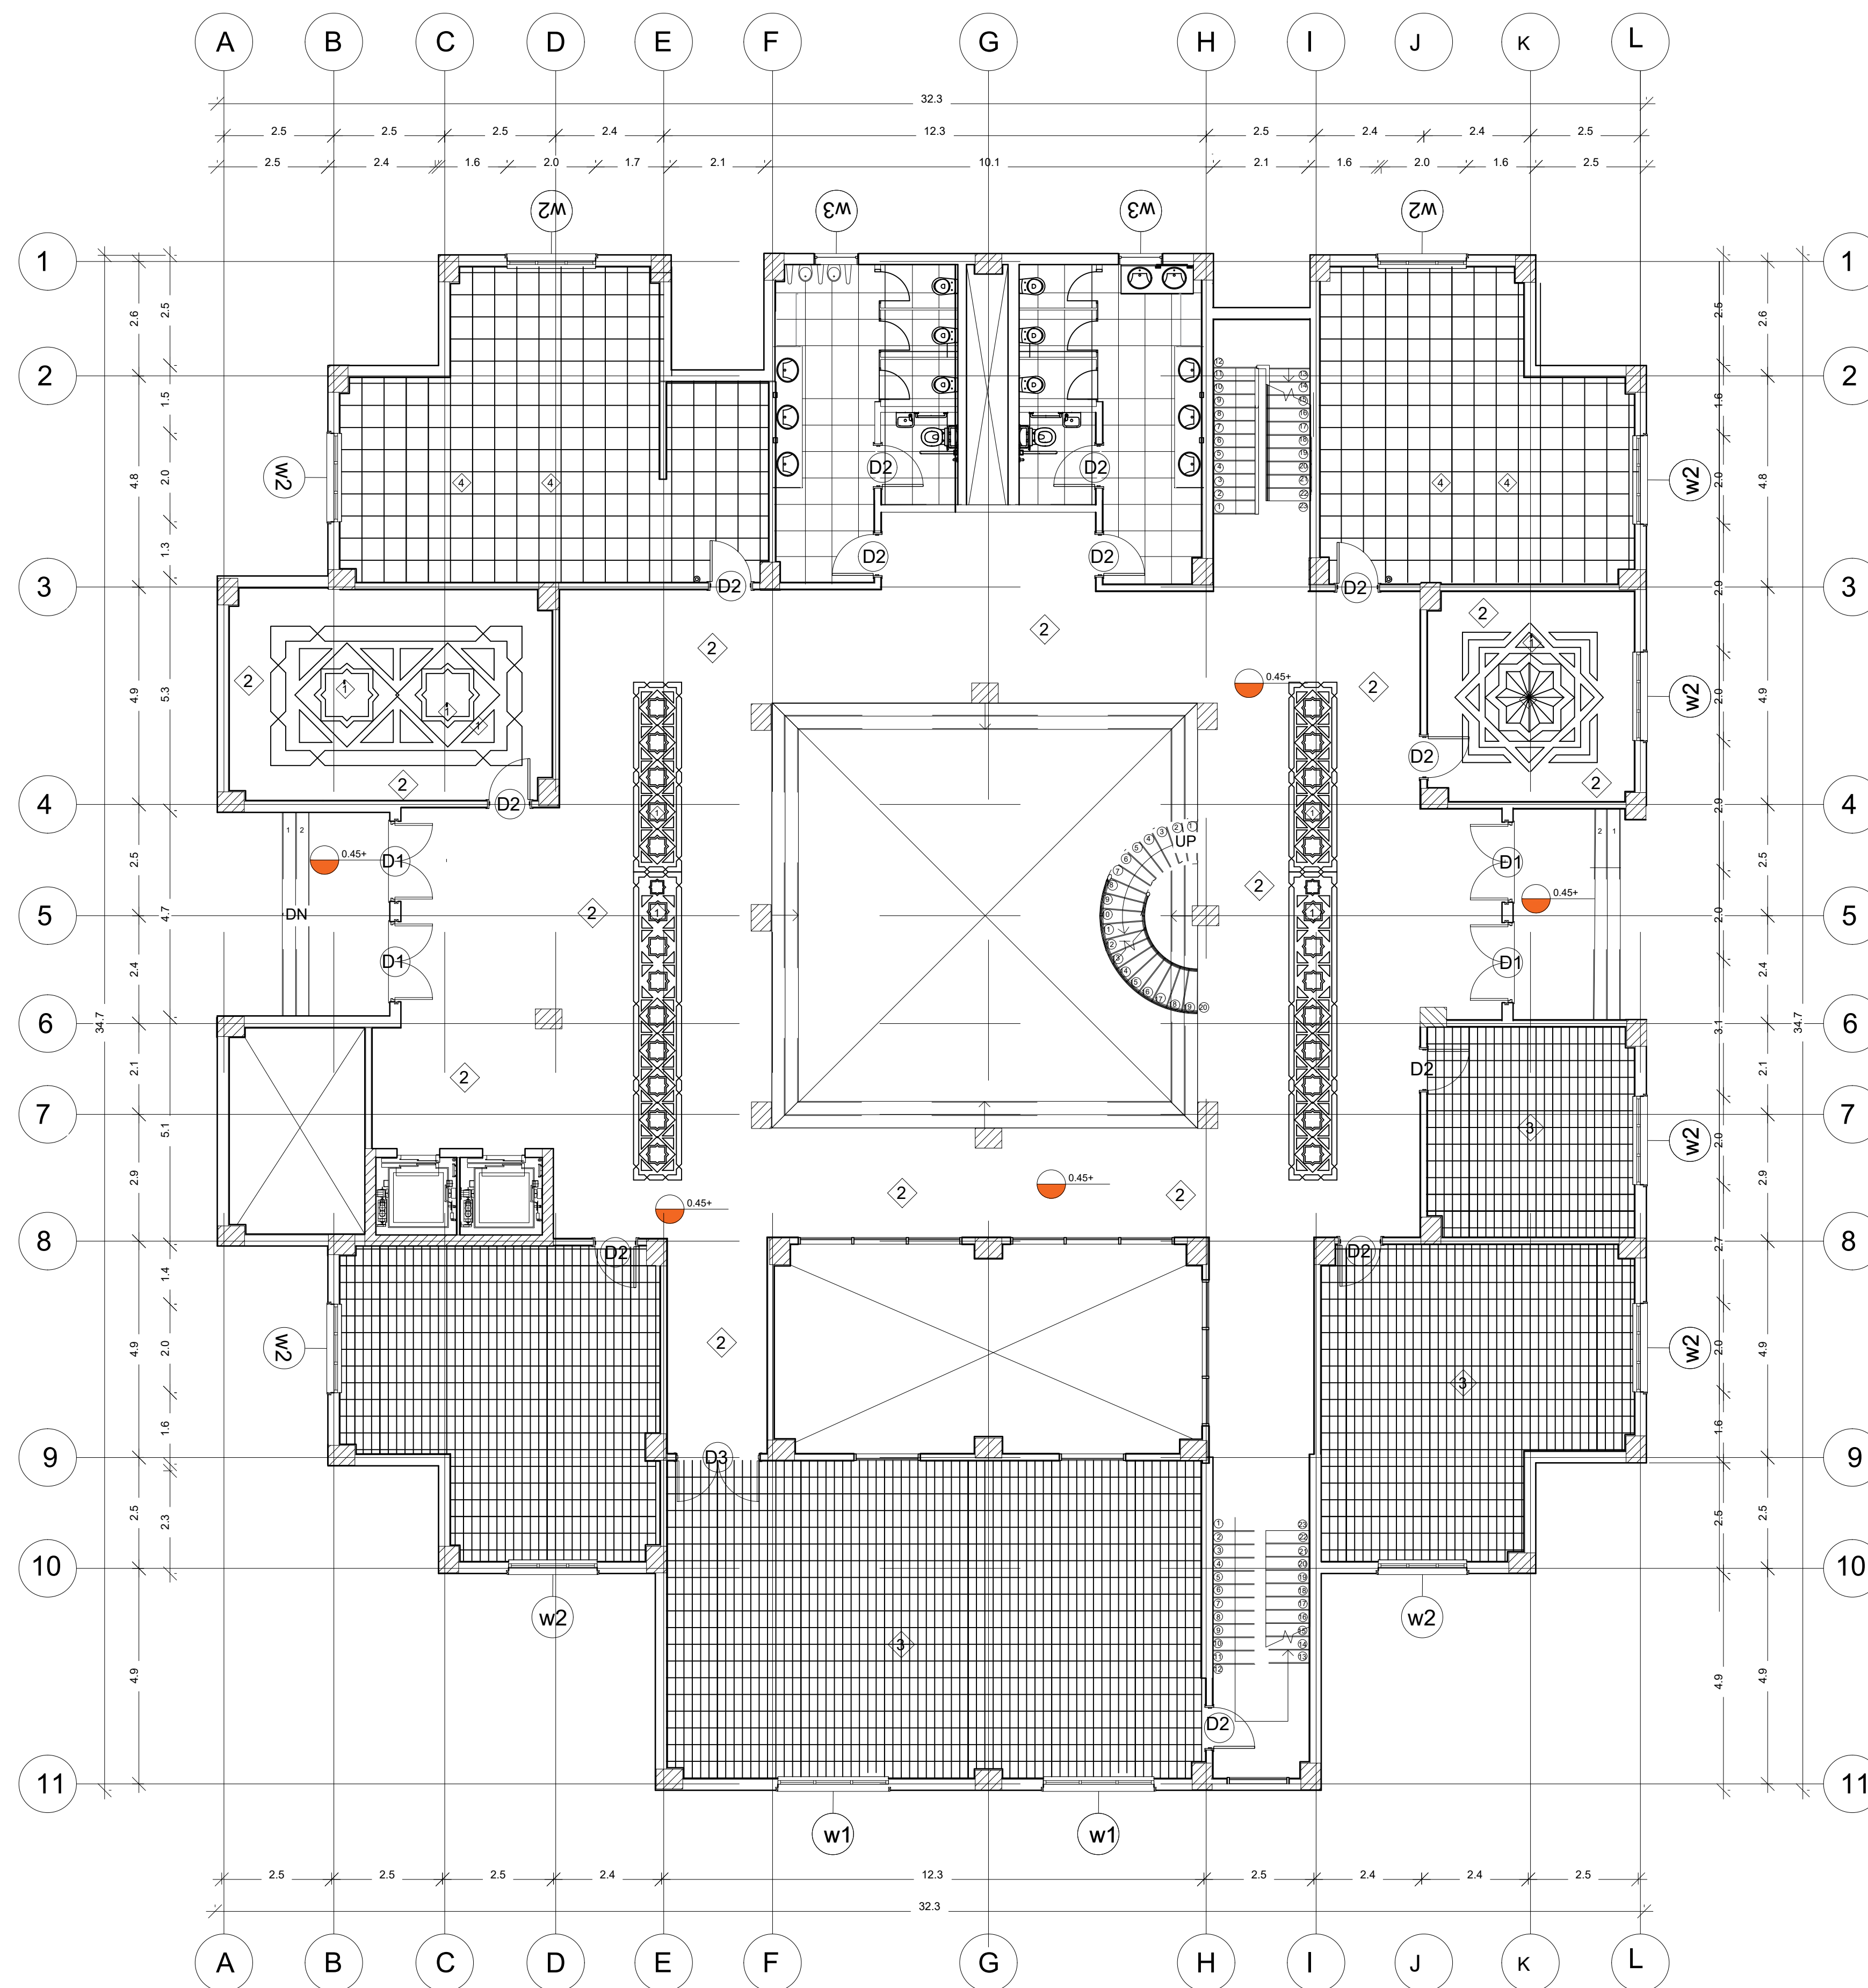

اسقف

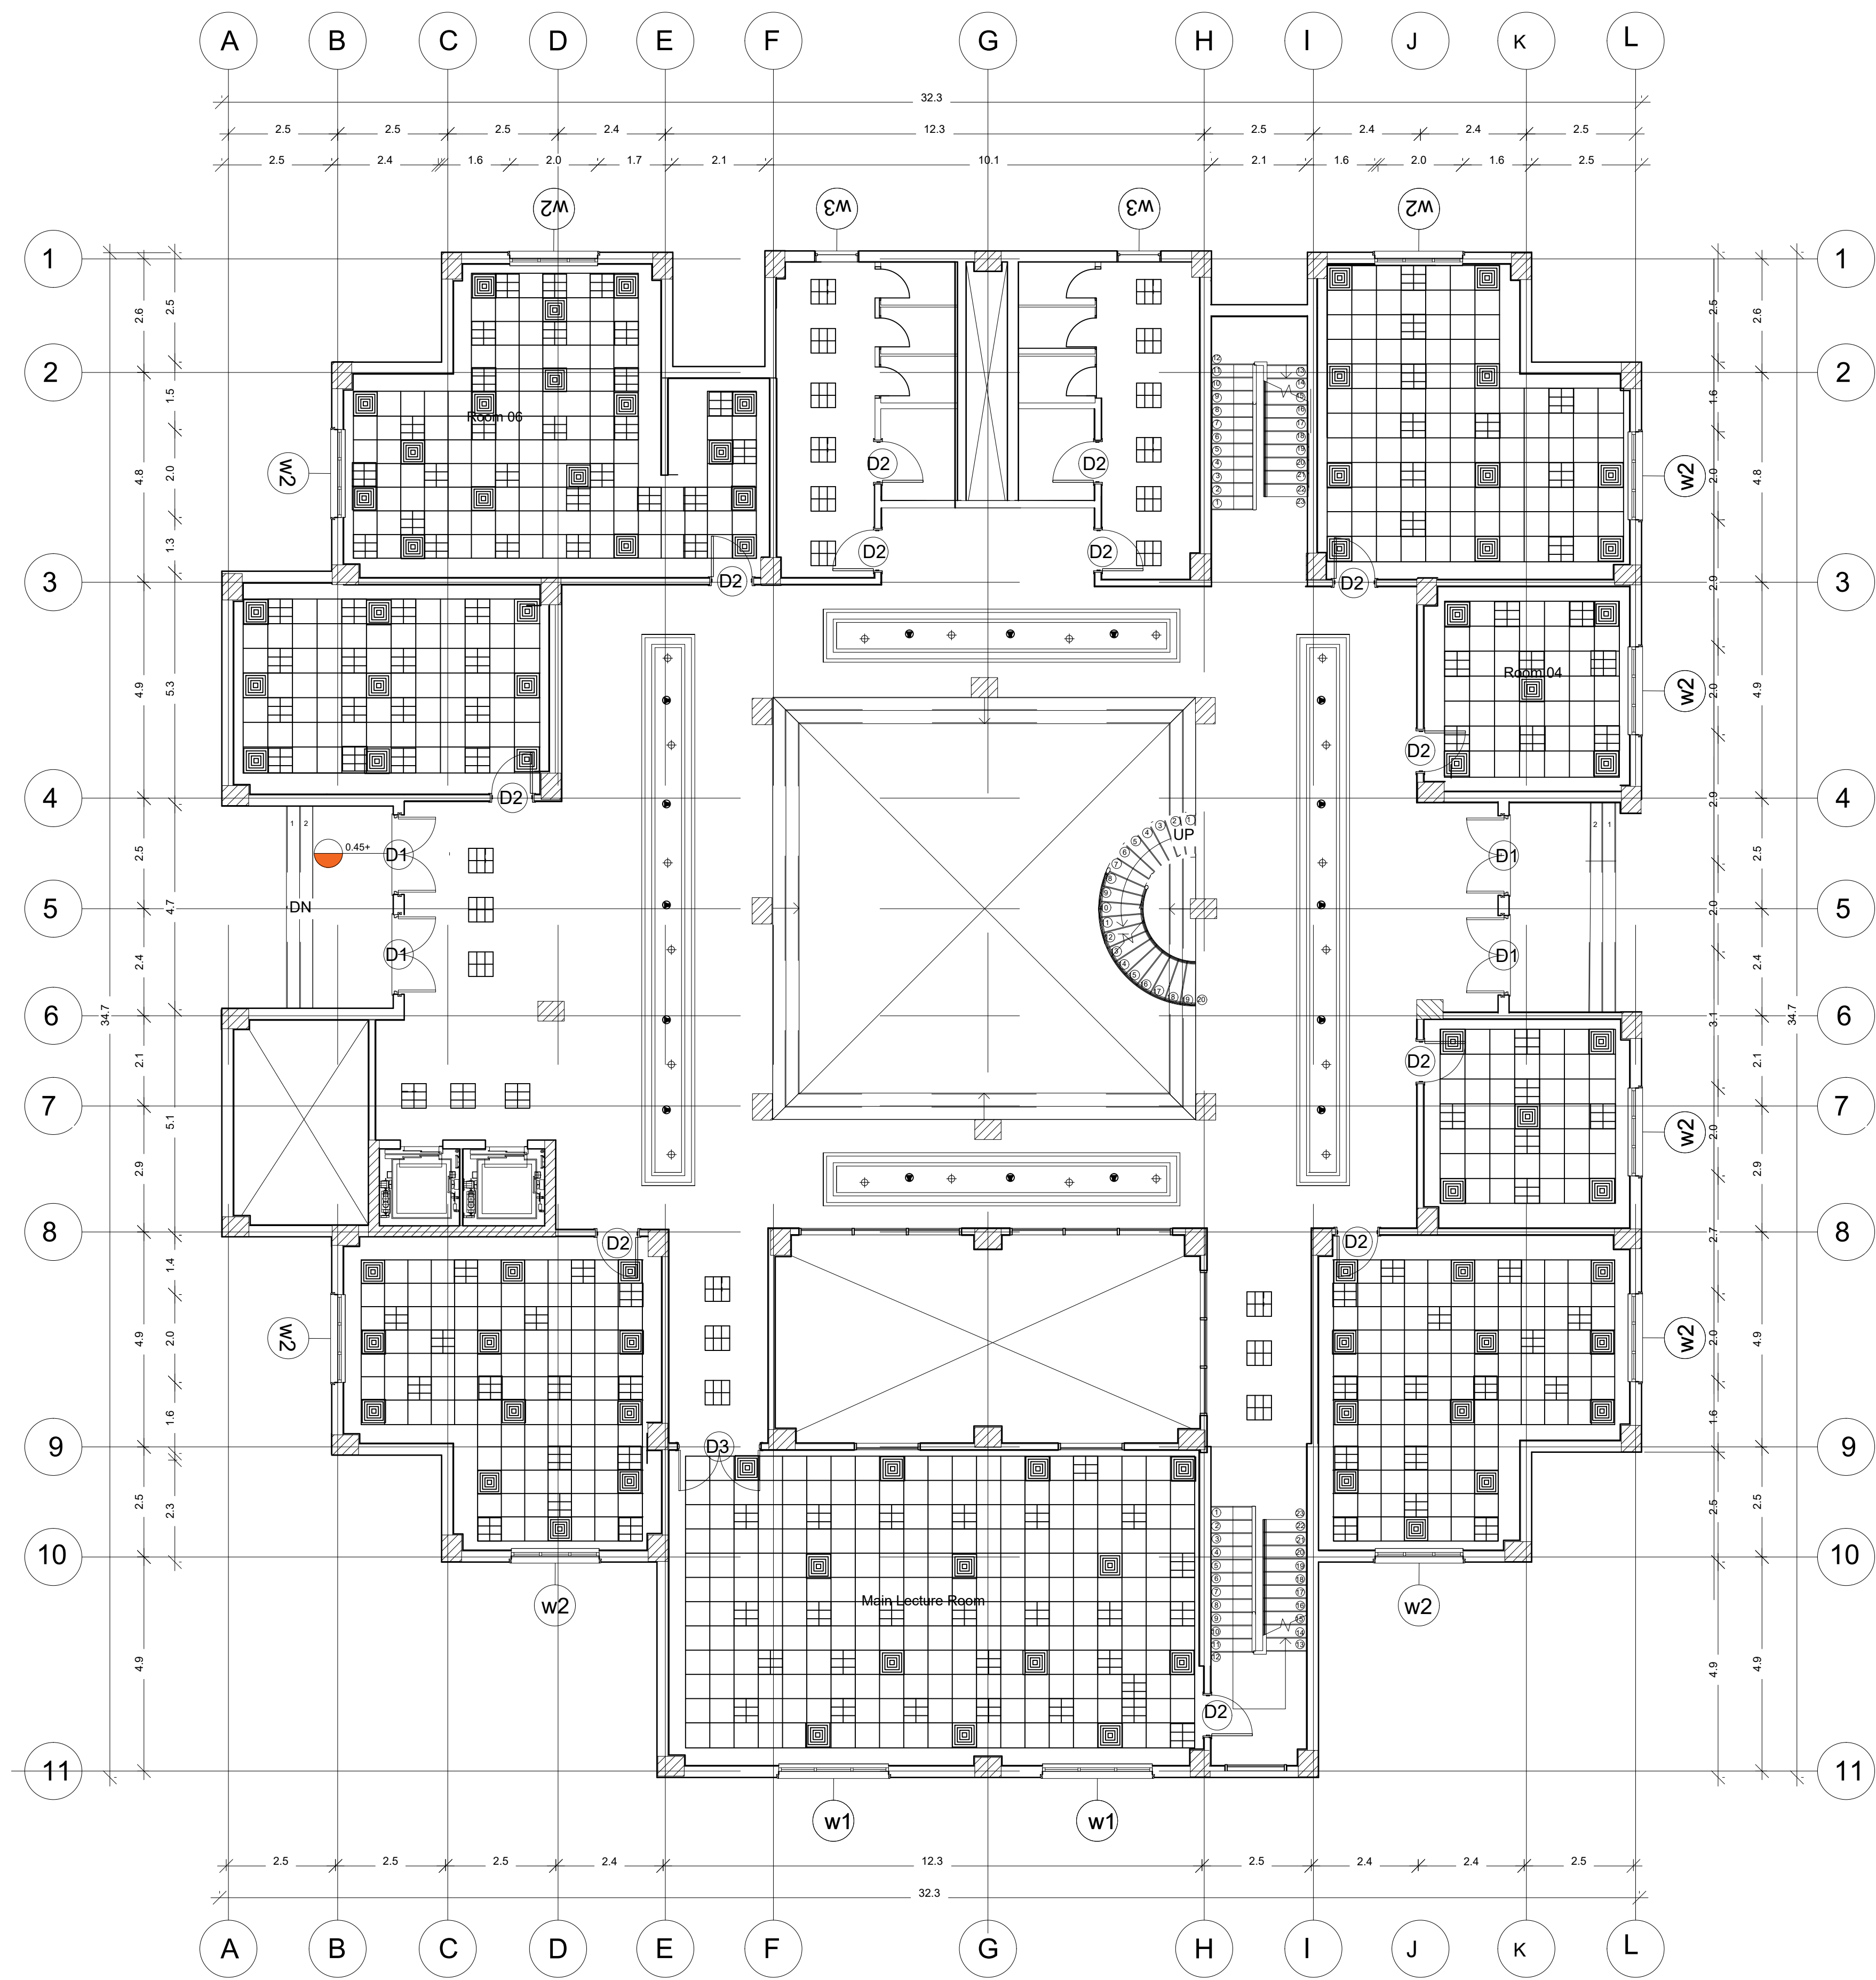


	air ventilation
	60*60cm suspended gypsum tiles
	Light 60*60

Youssef Hesham

52010801

checked by: Dr.Abdelrahman

Scale 1/100

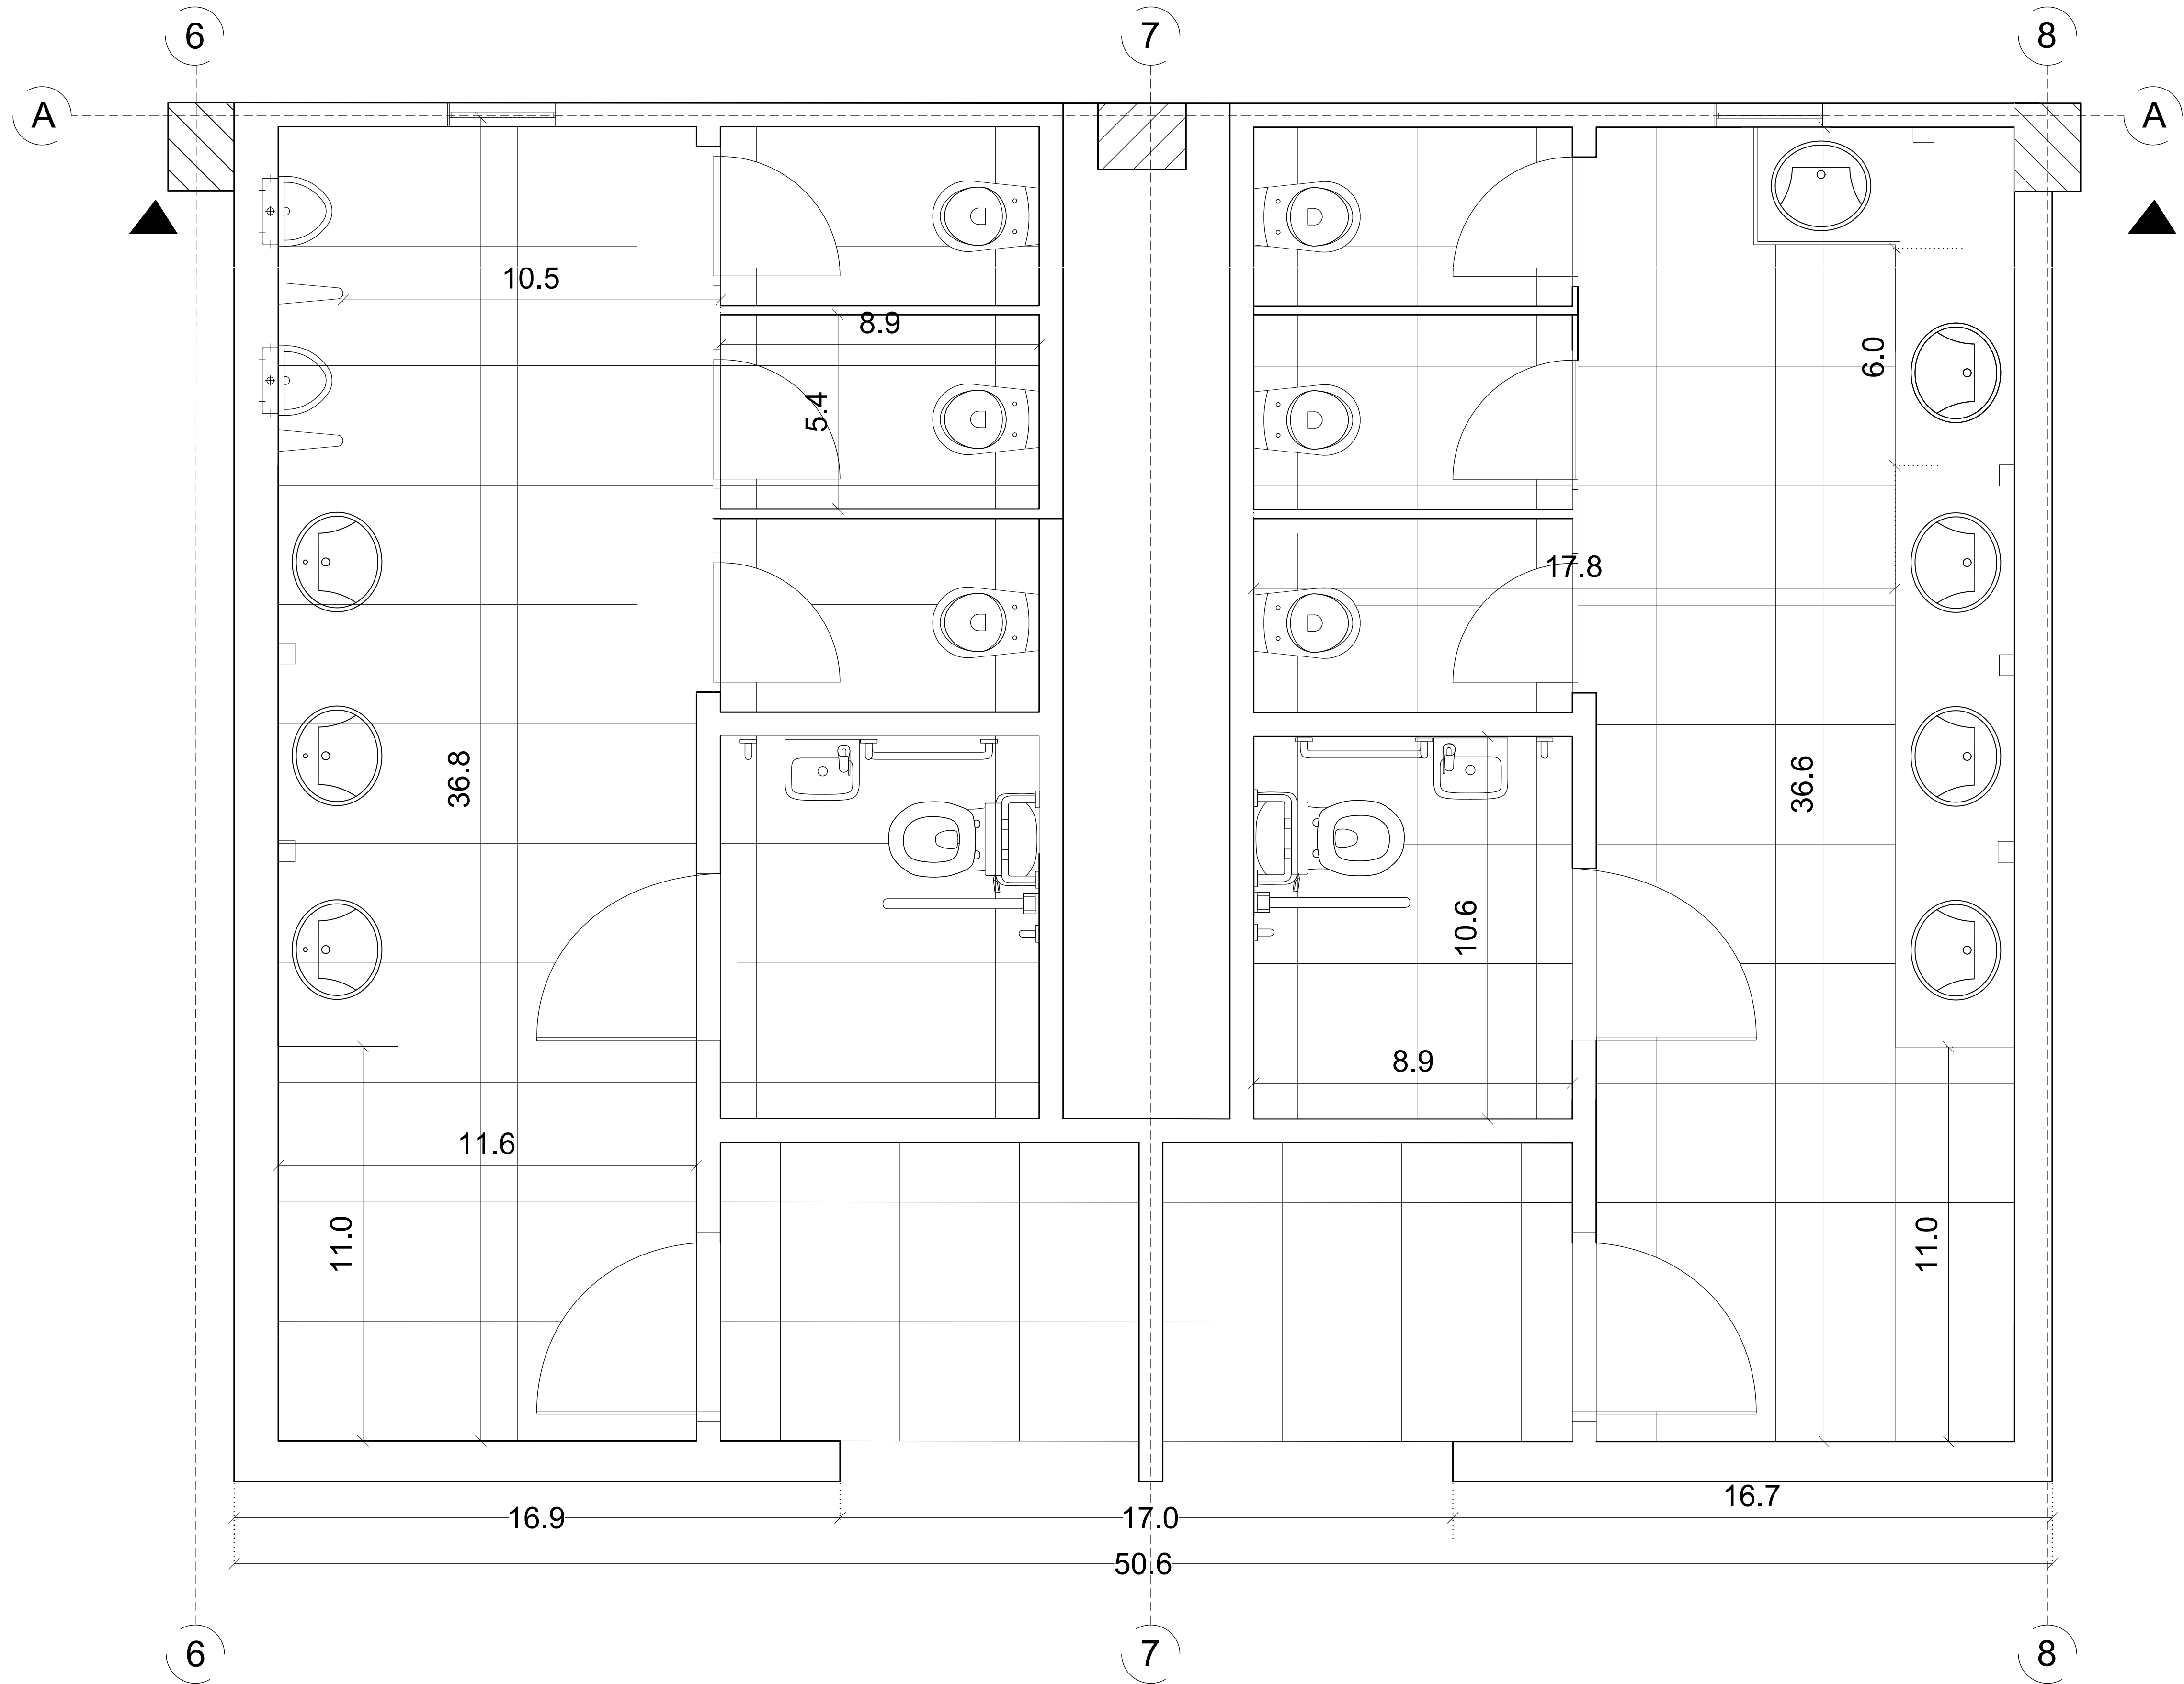

working 3


scale 1:20

drawn by: youssef hesham 52010801

cheked by: Dr.Abdulrahman

Date 29/7/2024

Stairs & elevator
plans

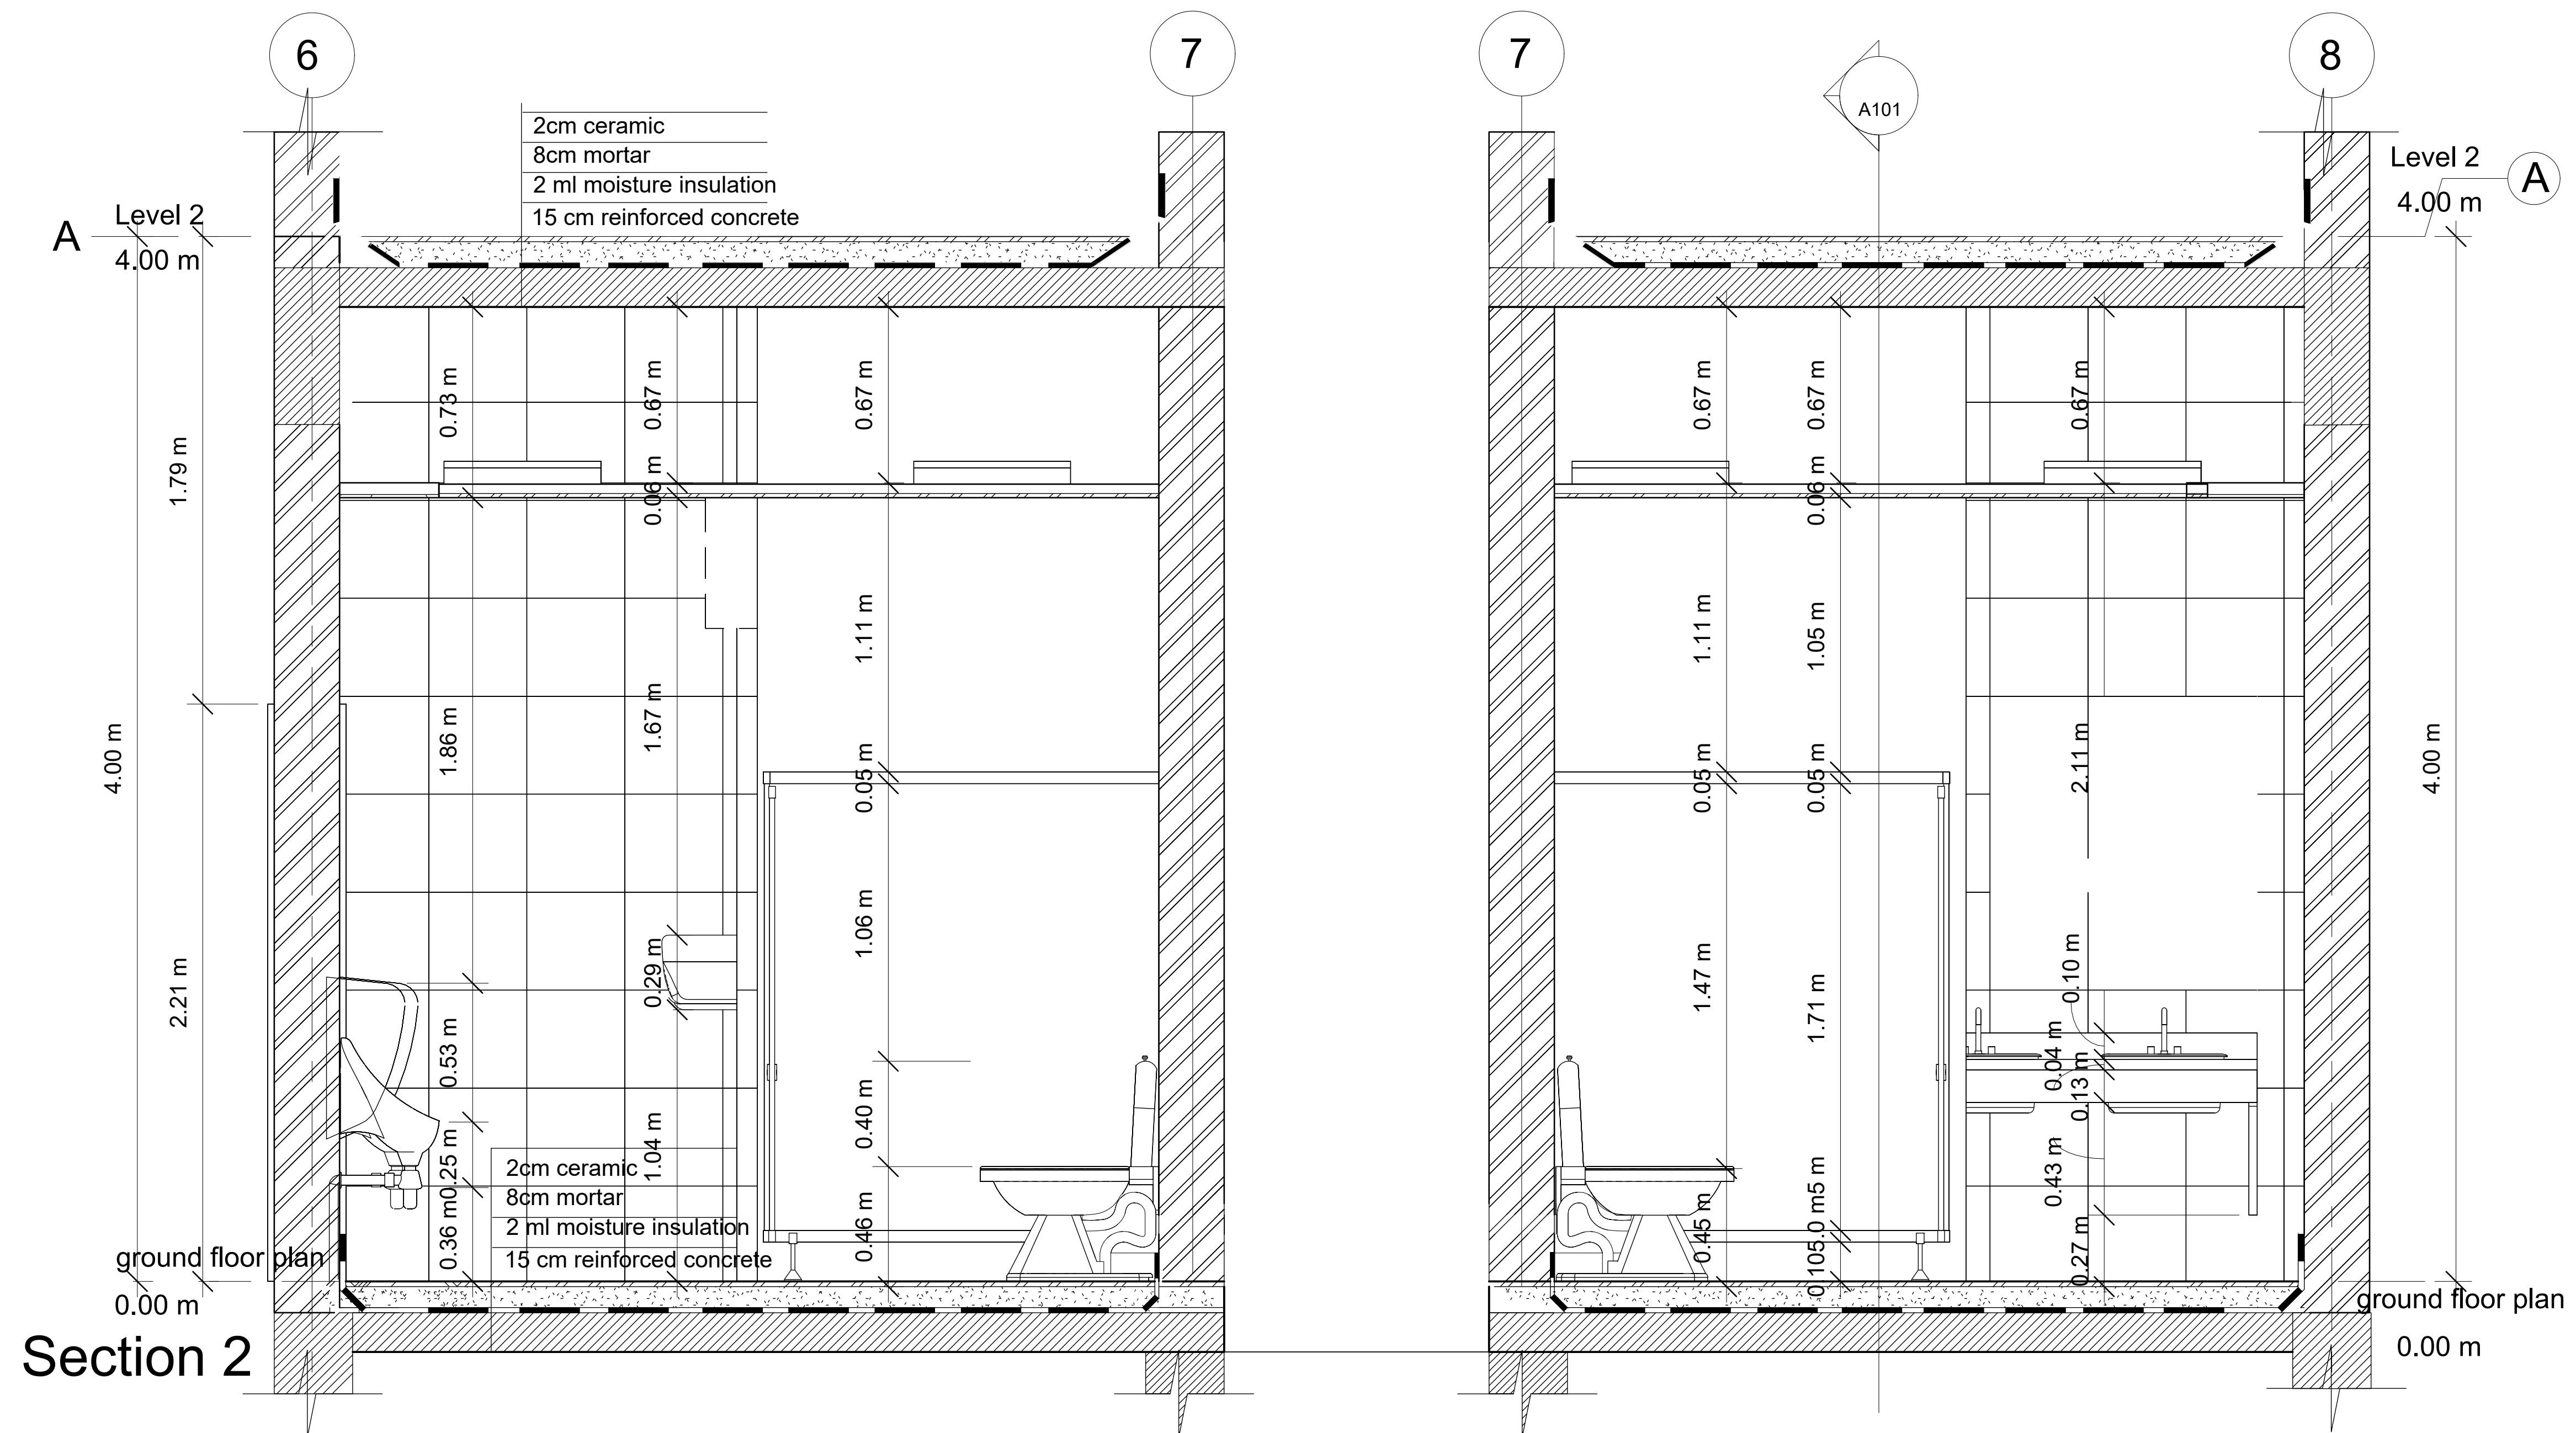

working 3


scale 1:20

drawn by: youssef hesham 52010801

checked by: Dr.Abdulrahman

Date 29/7/2024

Stairs & elevator
plans

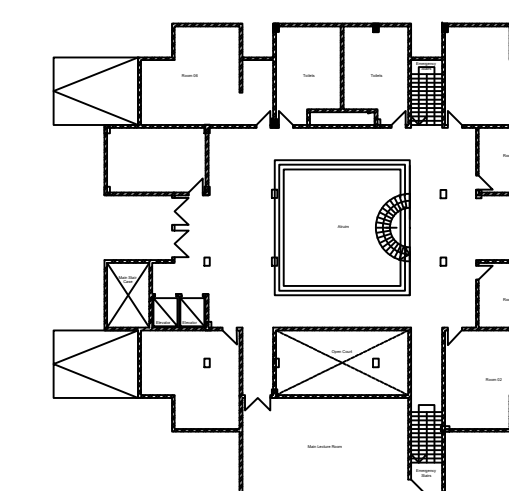


working 3





drawn by: youssef hesham 52010801

checked by: Dr.Abdelrahman

date: 19/8/2024

scale 1:20

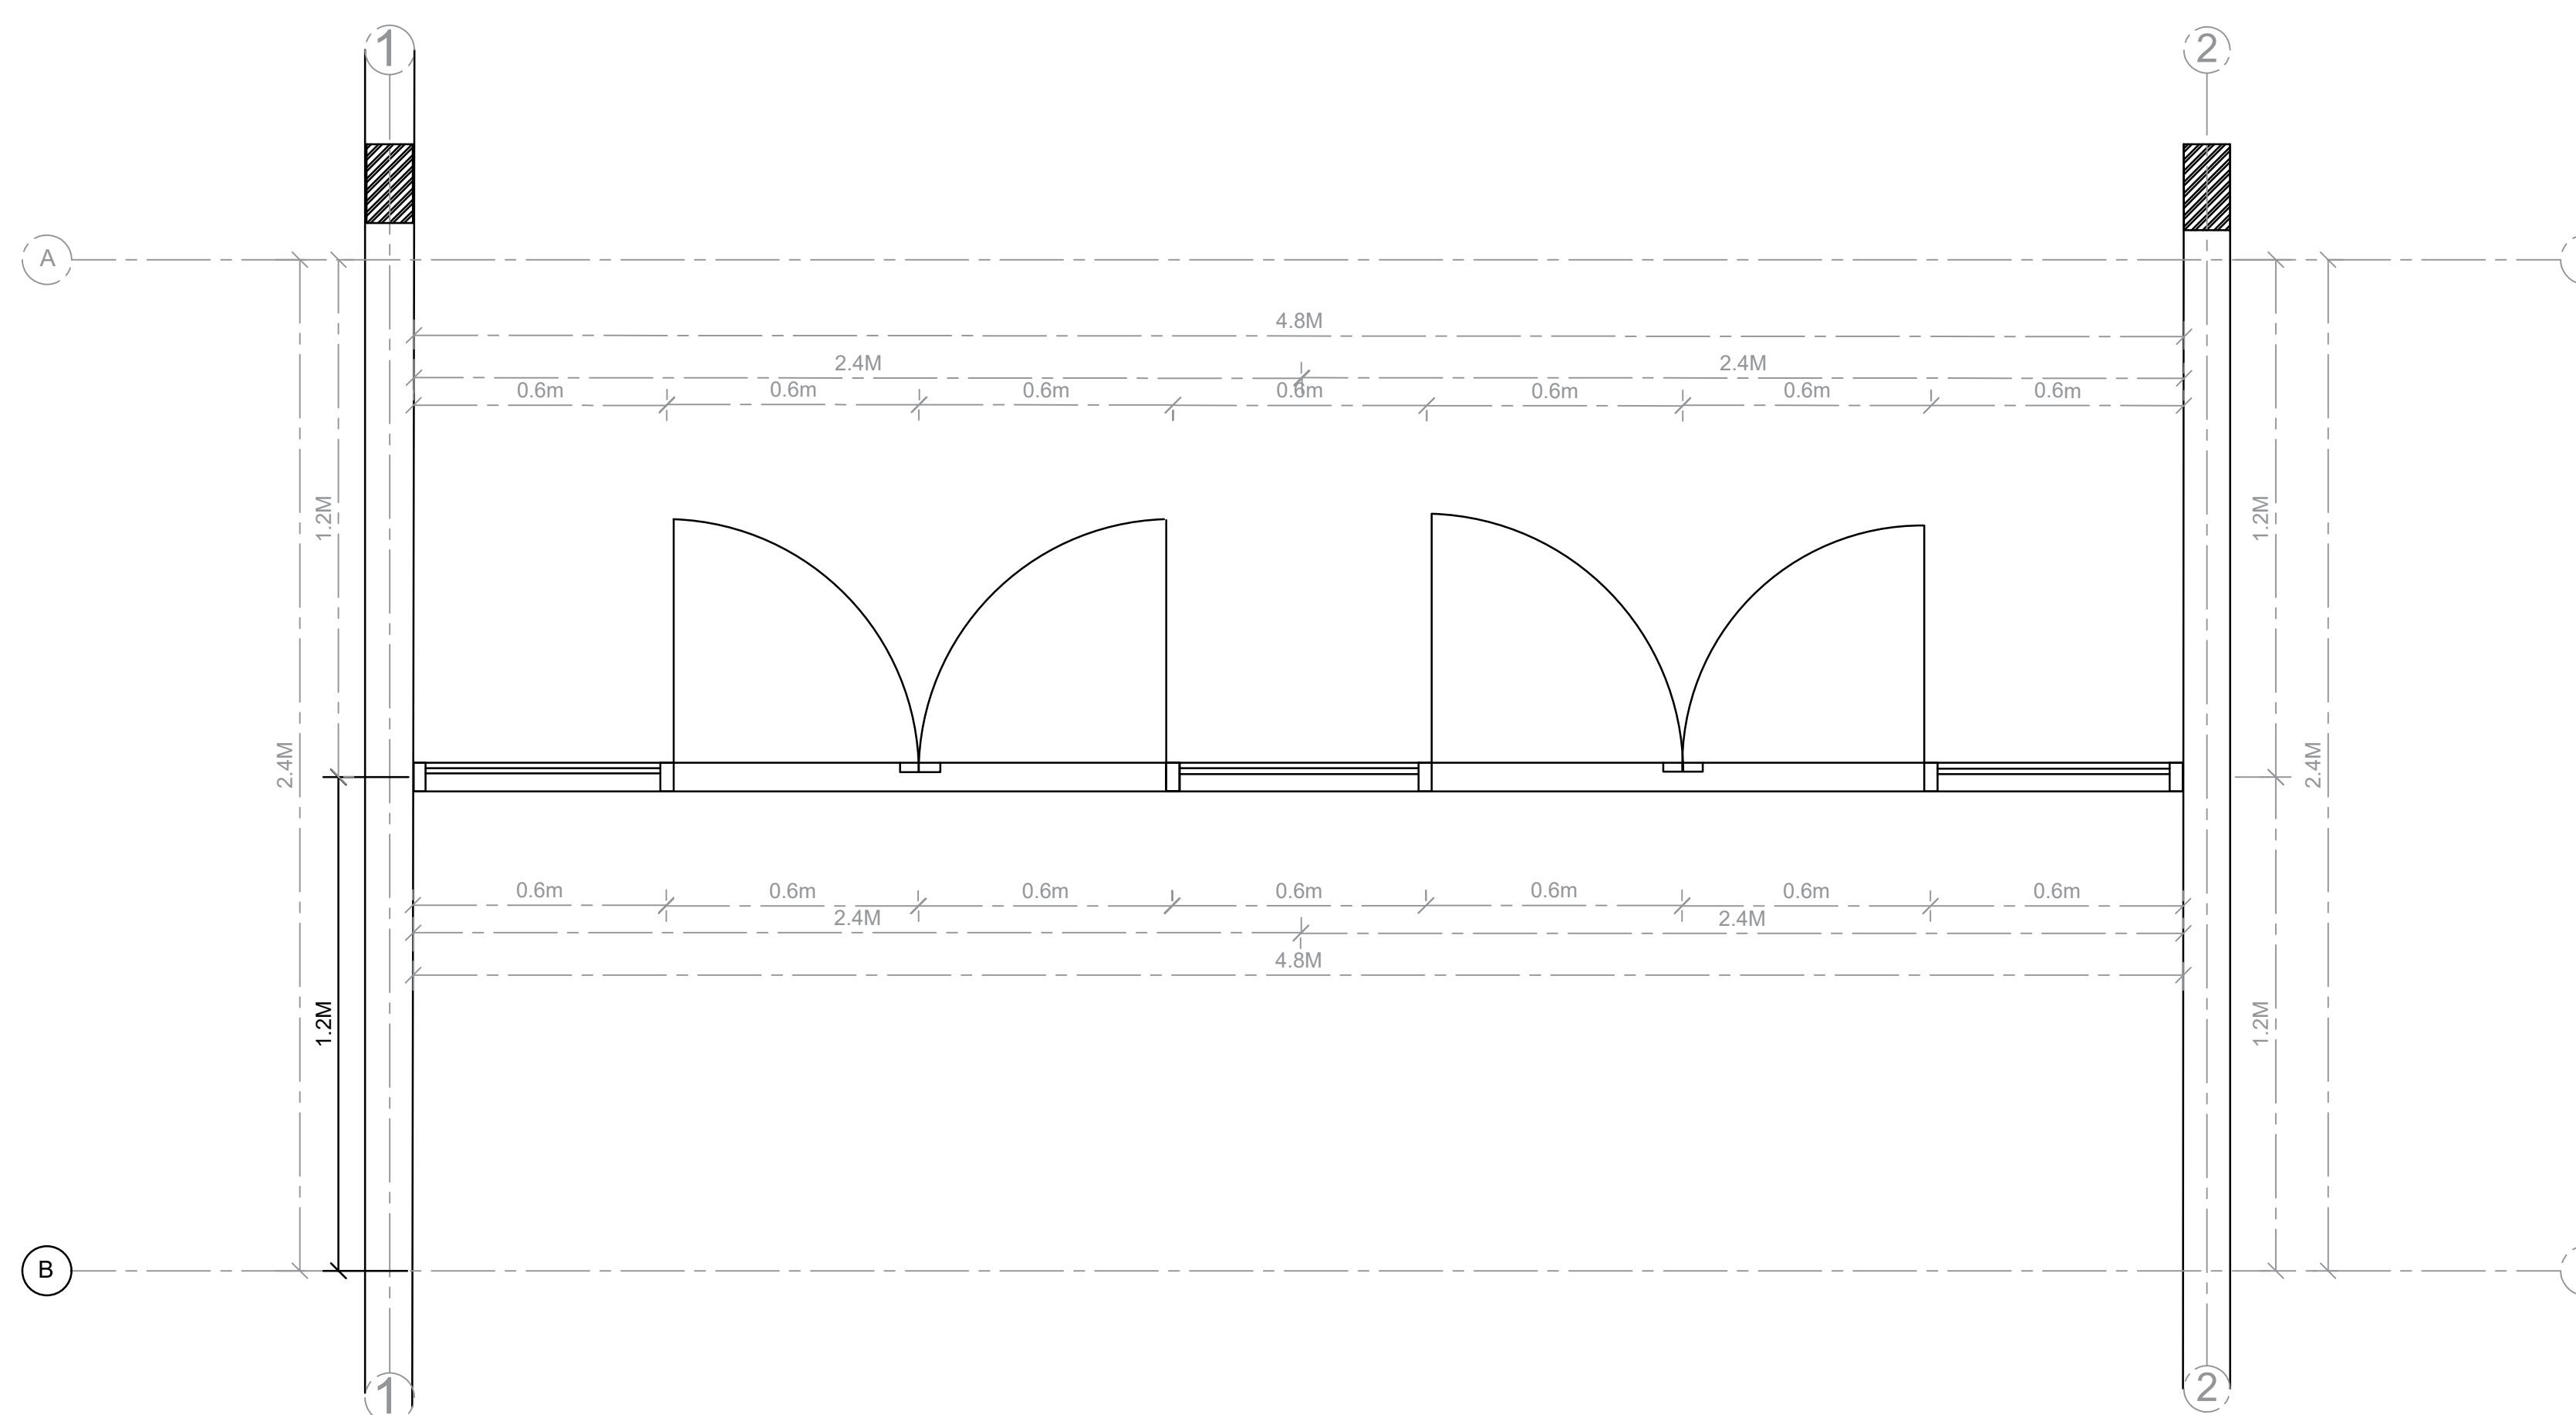

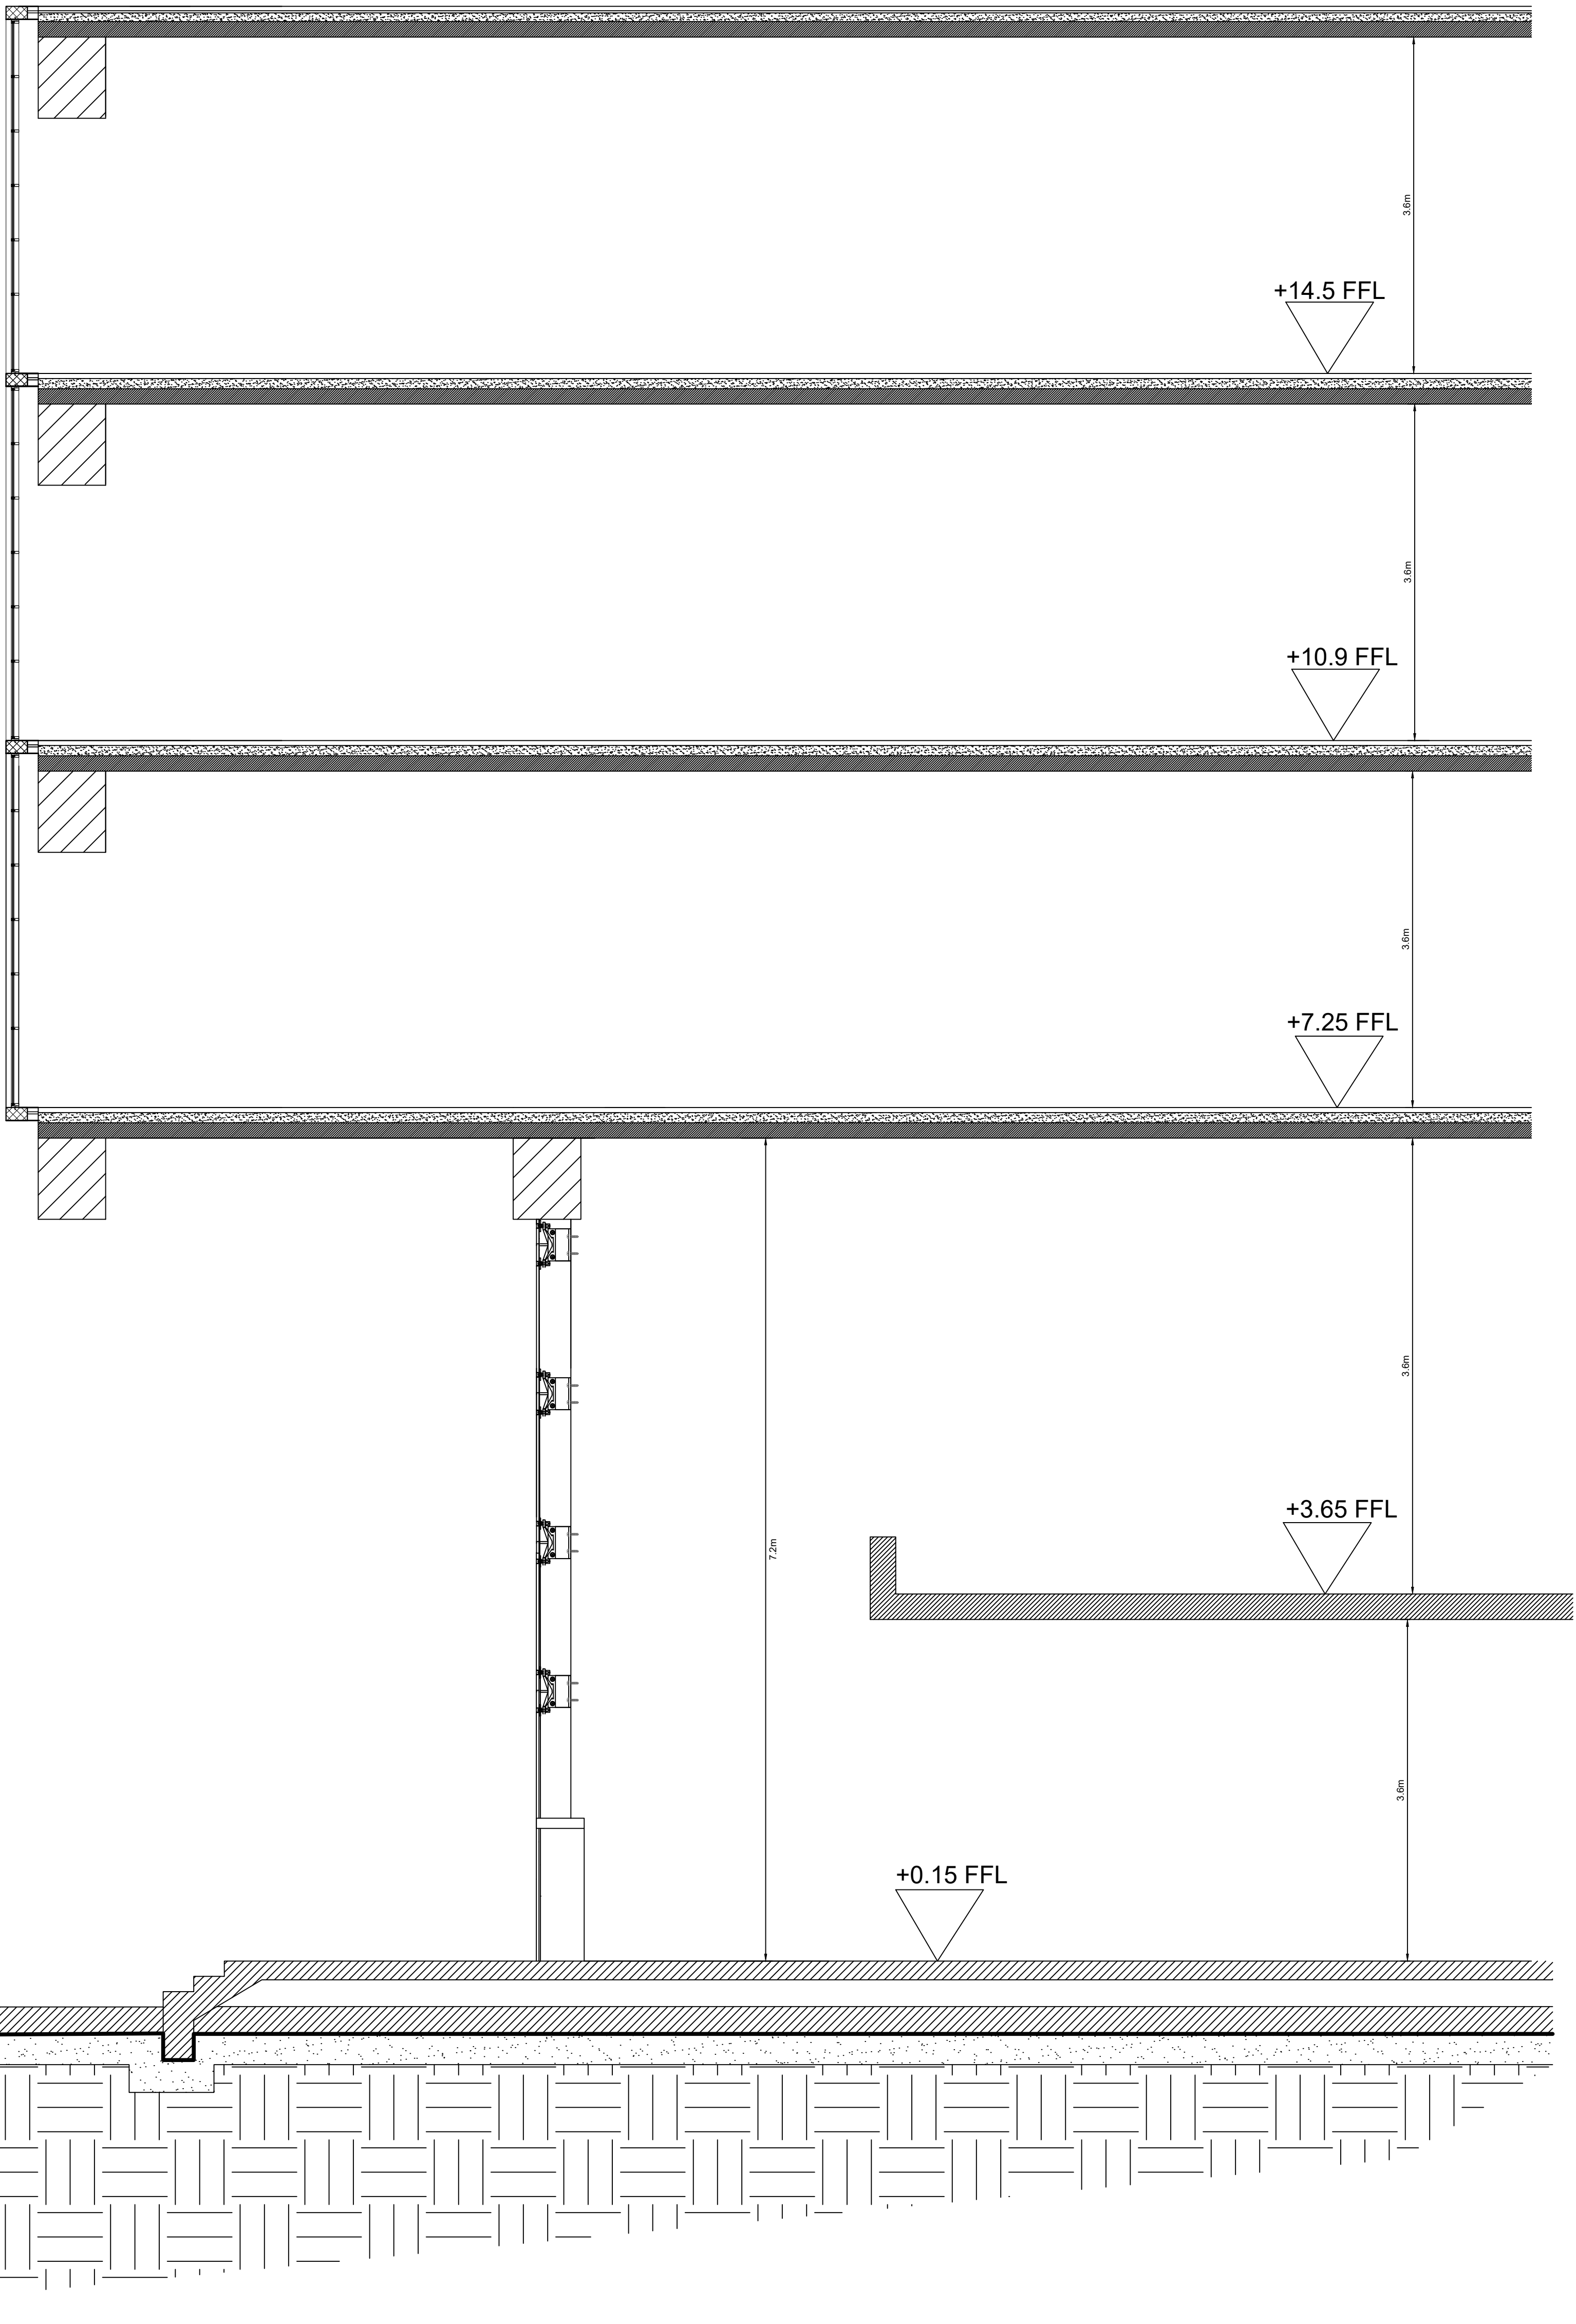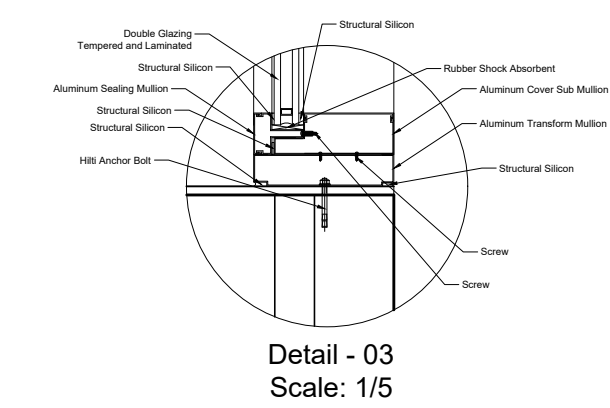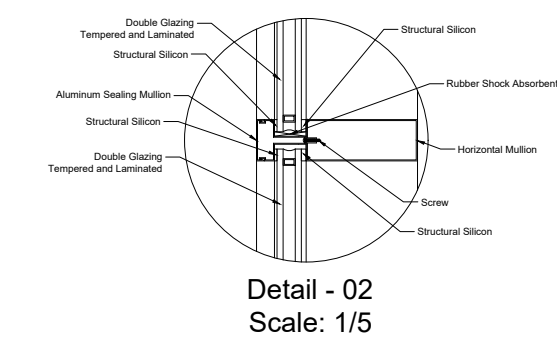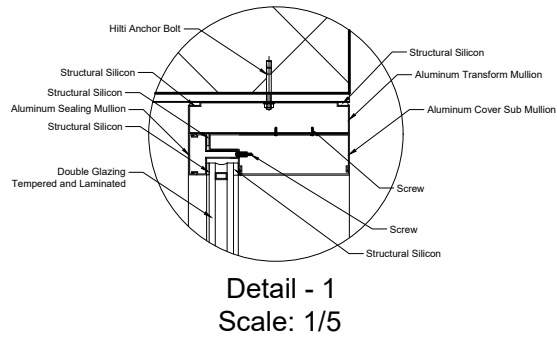

scale 1:20

Date
19/8/2024

drawn by: youssef hesham 52010801

cheked by: Dr.Abdulrahman

working 3

