


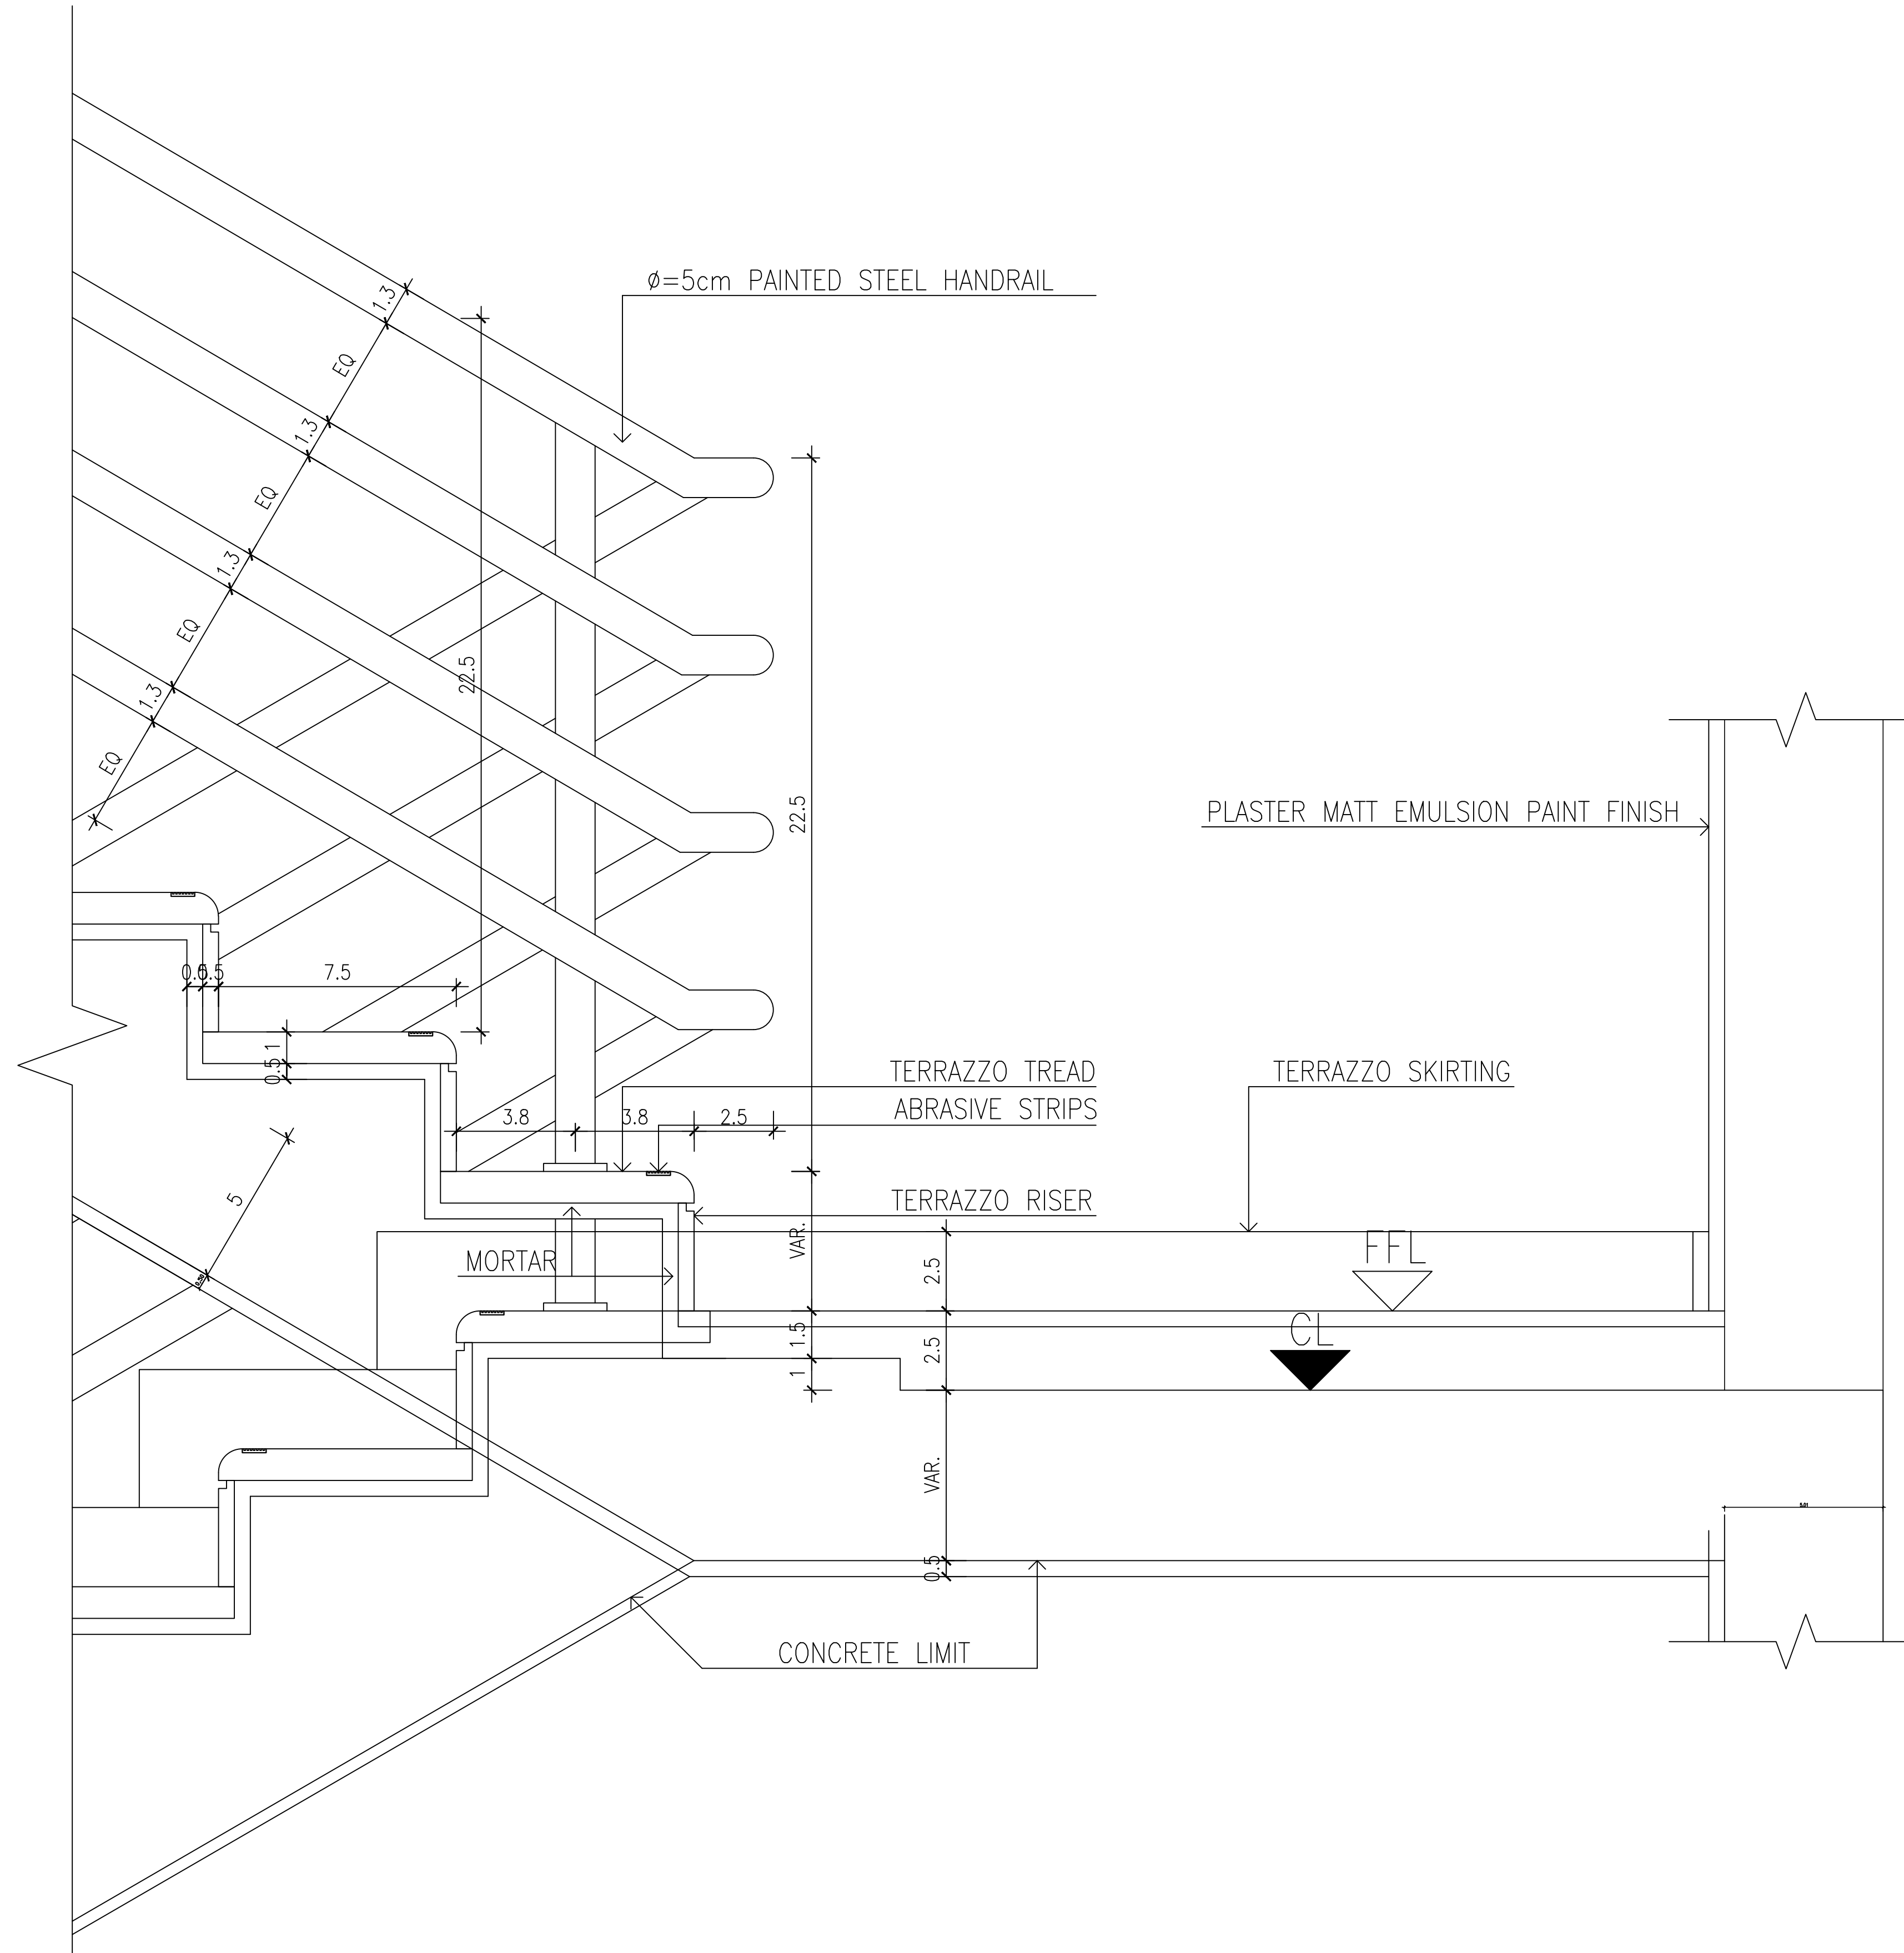

ACU

working 3


scale 1:5

drawn by: youssef hesham 52010801


cheked by: Dr.Abdulrahman

Date 29/7/2024


ACU

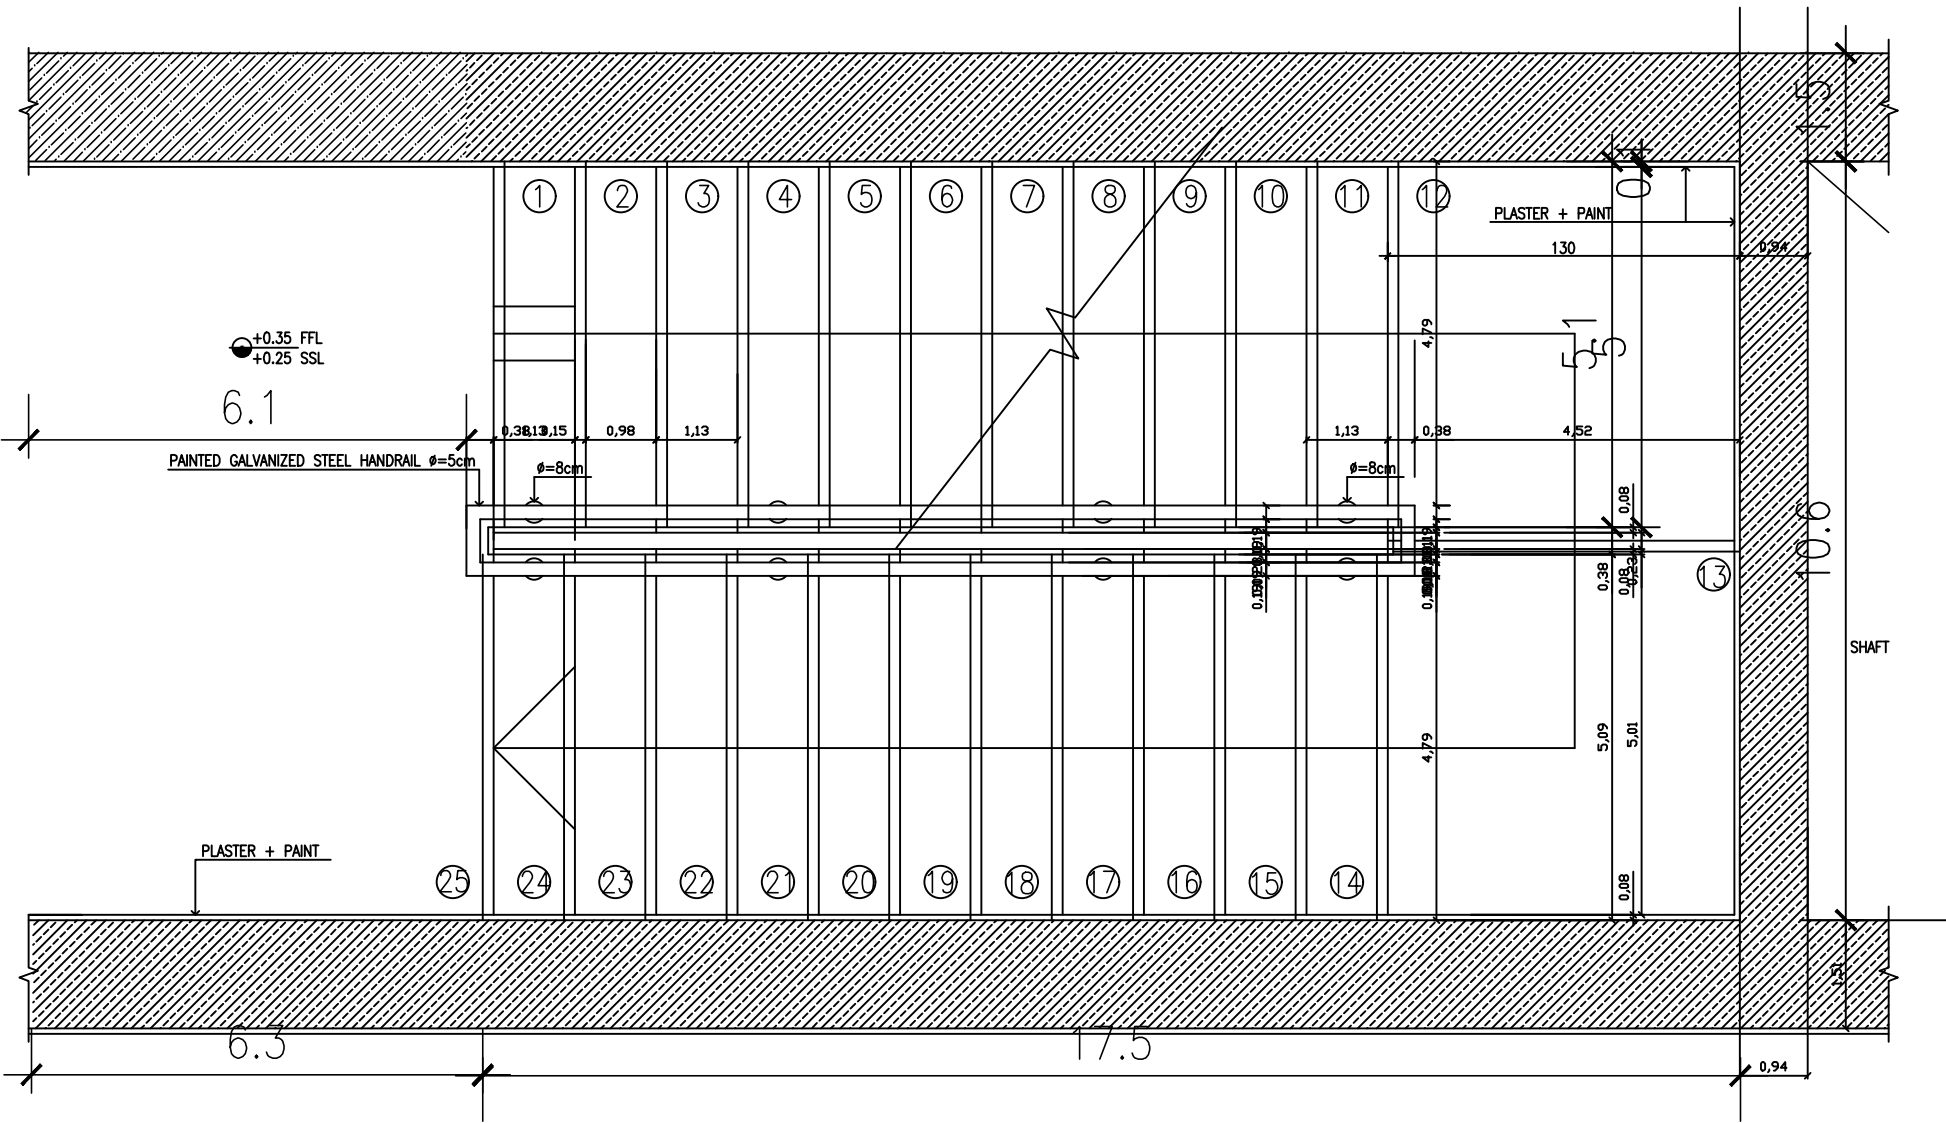

Stairs plan 1:20

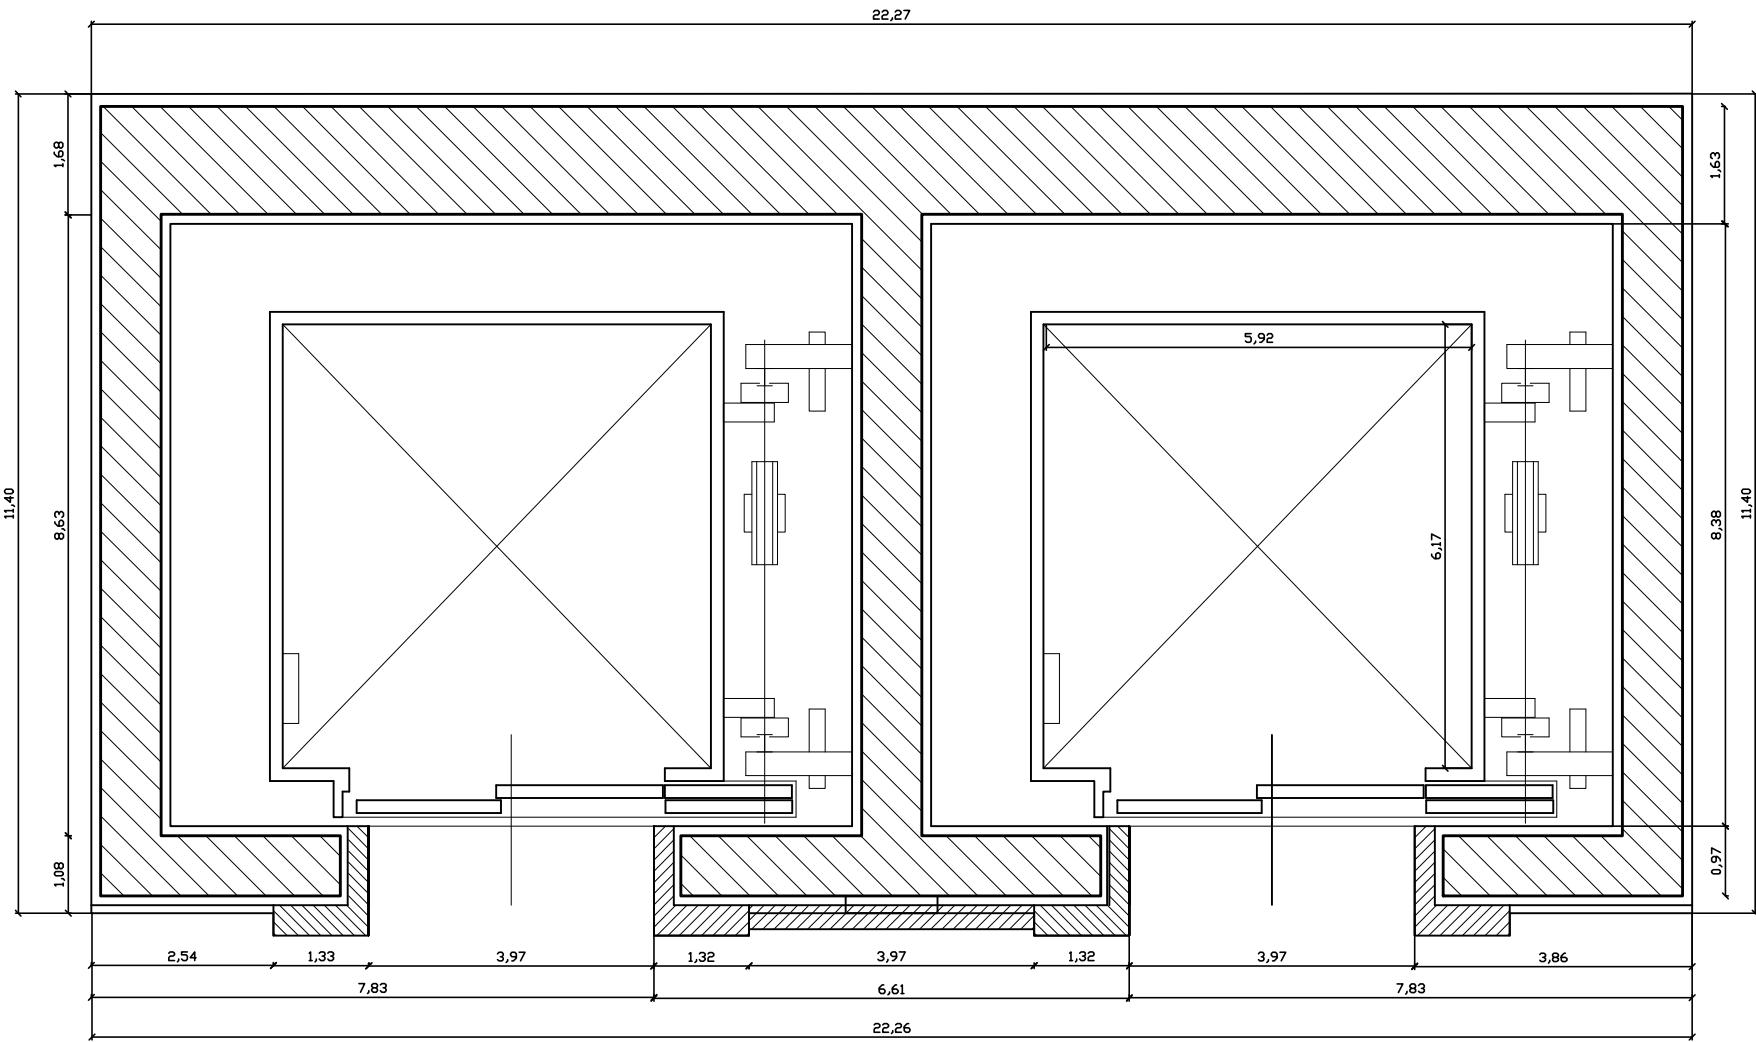

elevator plan 1:20

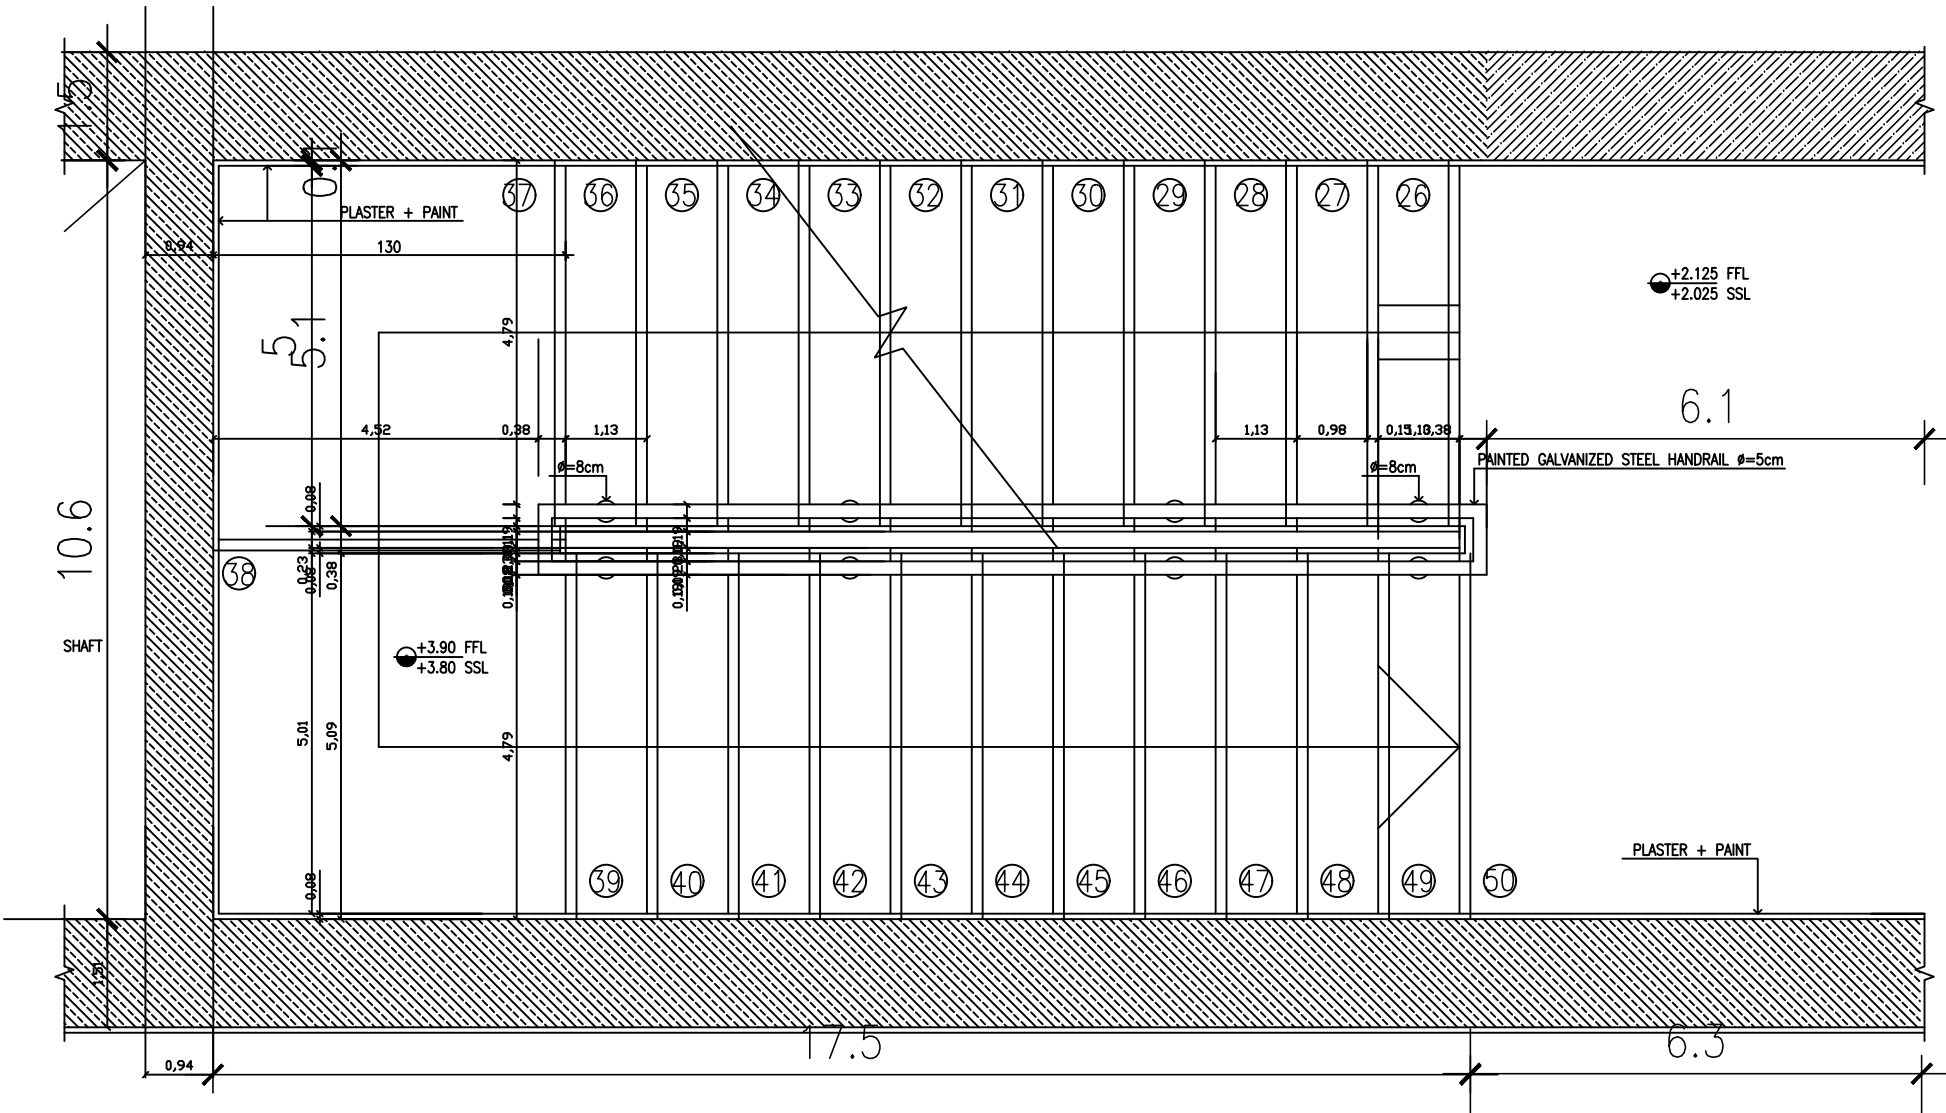

Stairs plan 1:20

working 3


scale 1:20

drawn by: yousef hesham 52010801

cheked by: Dr.Abdulrahman

Date 29/7/2024

Stairs & elevator plans

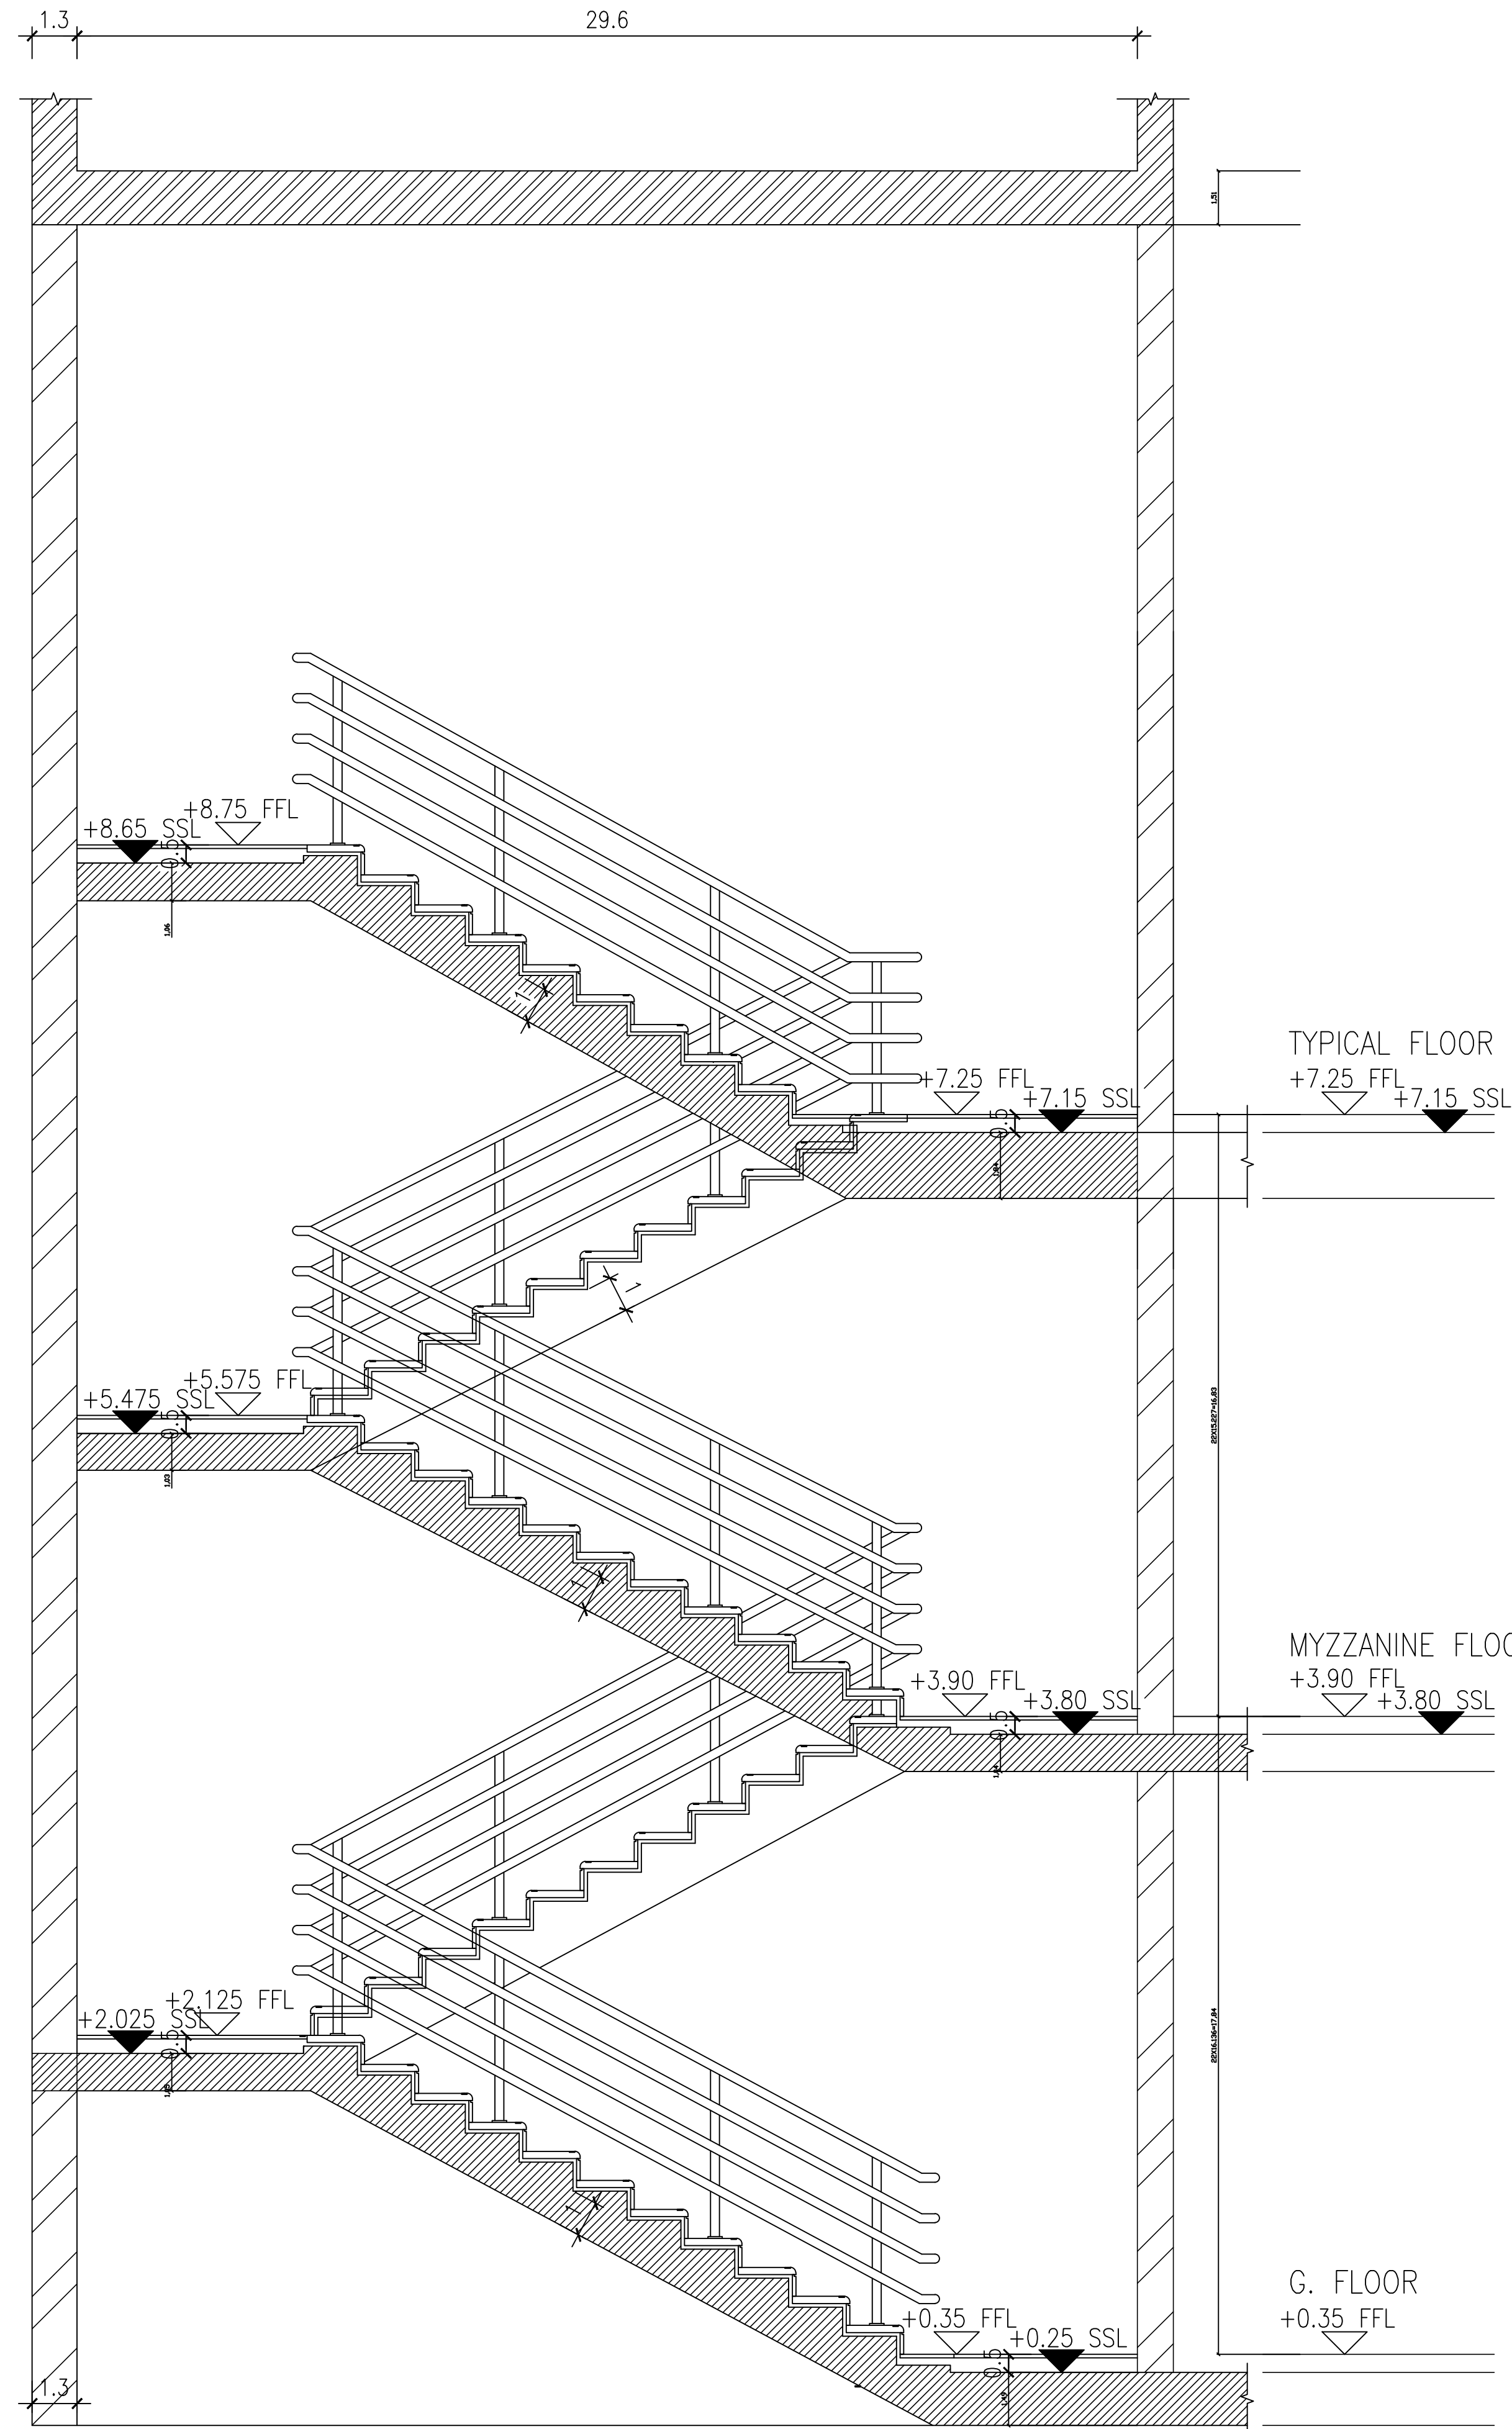

Stairs section 1:20

ACU

working 3

scale 1:20

drawn by: youssef hesham 52010801

cheked by: Dr.Abdulrahman

Date 29/7/2024